X02-K-03.01
SOUFFLANTE DU SECHEUR DE REACTIVATION
DRIER REACTIVATION BLOWER
DEBIT NOMINALE : 21935 Nm³ /h : RATED FLOW
PRESSION DIFFERENTIELLE : 3.9 BAR : DIFFERENTIAL PRESSURE

X02-G-03.14
SEPARATEUR DU SECHEUR DE REACTIVATION
DRIER REACTIVATION SEPARATOR
650 DIA x 2500 T/T
PRESSION NOMINALE : 49.7 BARG : DESIGN PRESSURE
TEMP. NOMINALE : 290°C : DESIGN TEMP.

X02-E-03.15
REFROIDISSEUR DU SECHEUR DE REACTIVATION
DRIER REACTIVATION COOLER
CAPACITE : 3209 kW : CAPACITY
PRESSION NOMINALE : 49.7 BARG : DESIGN PRESSURE
TEMP. NOMINALE : 310°C : DESIGN TEMP.

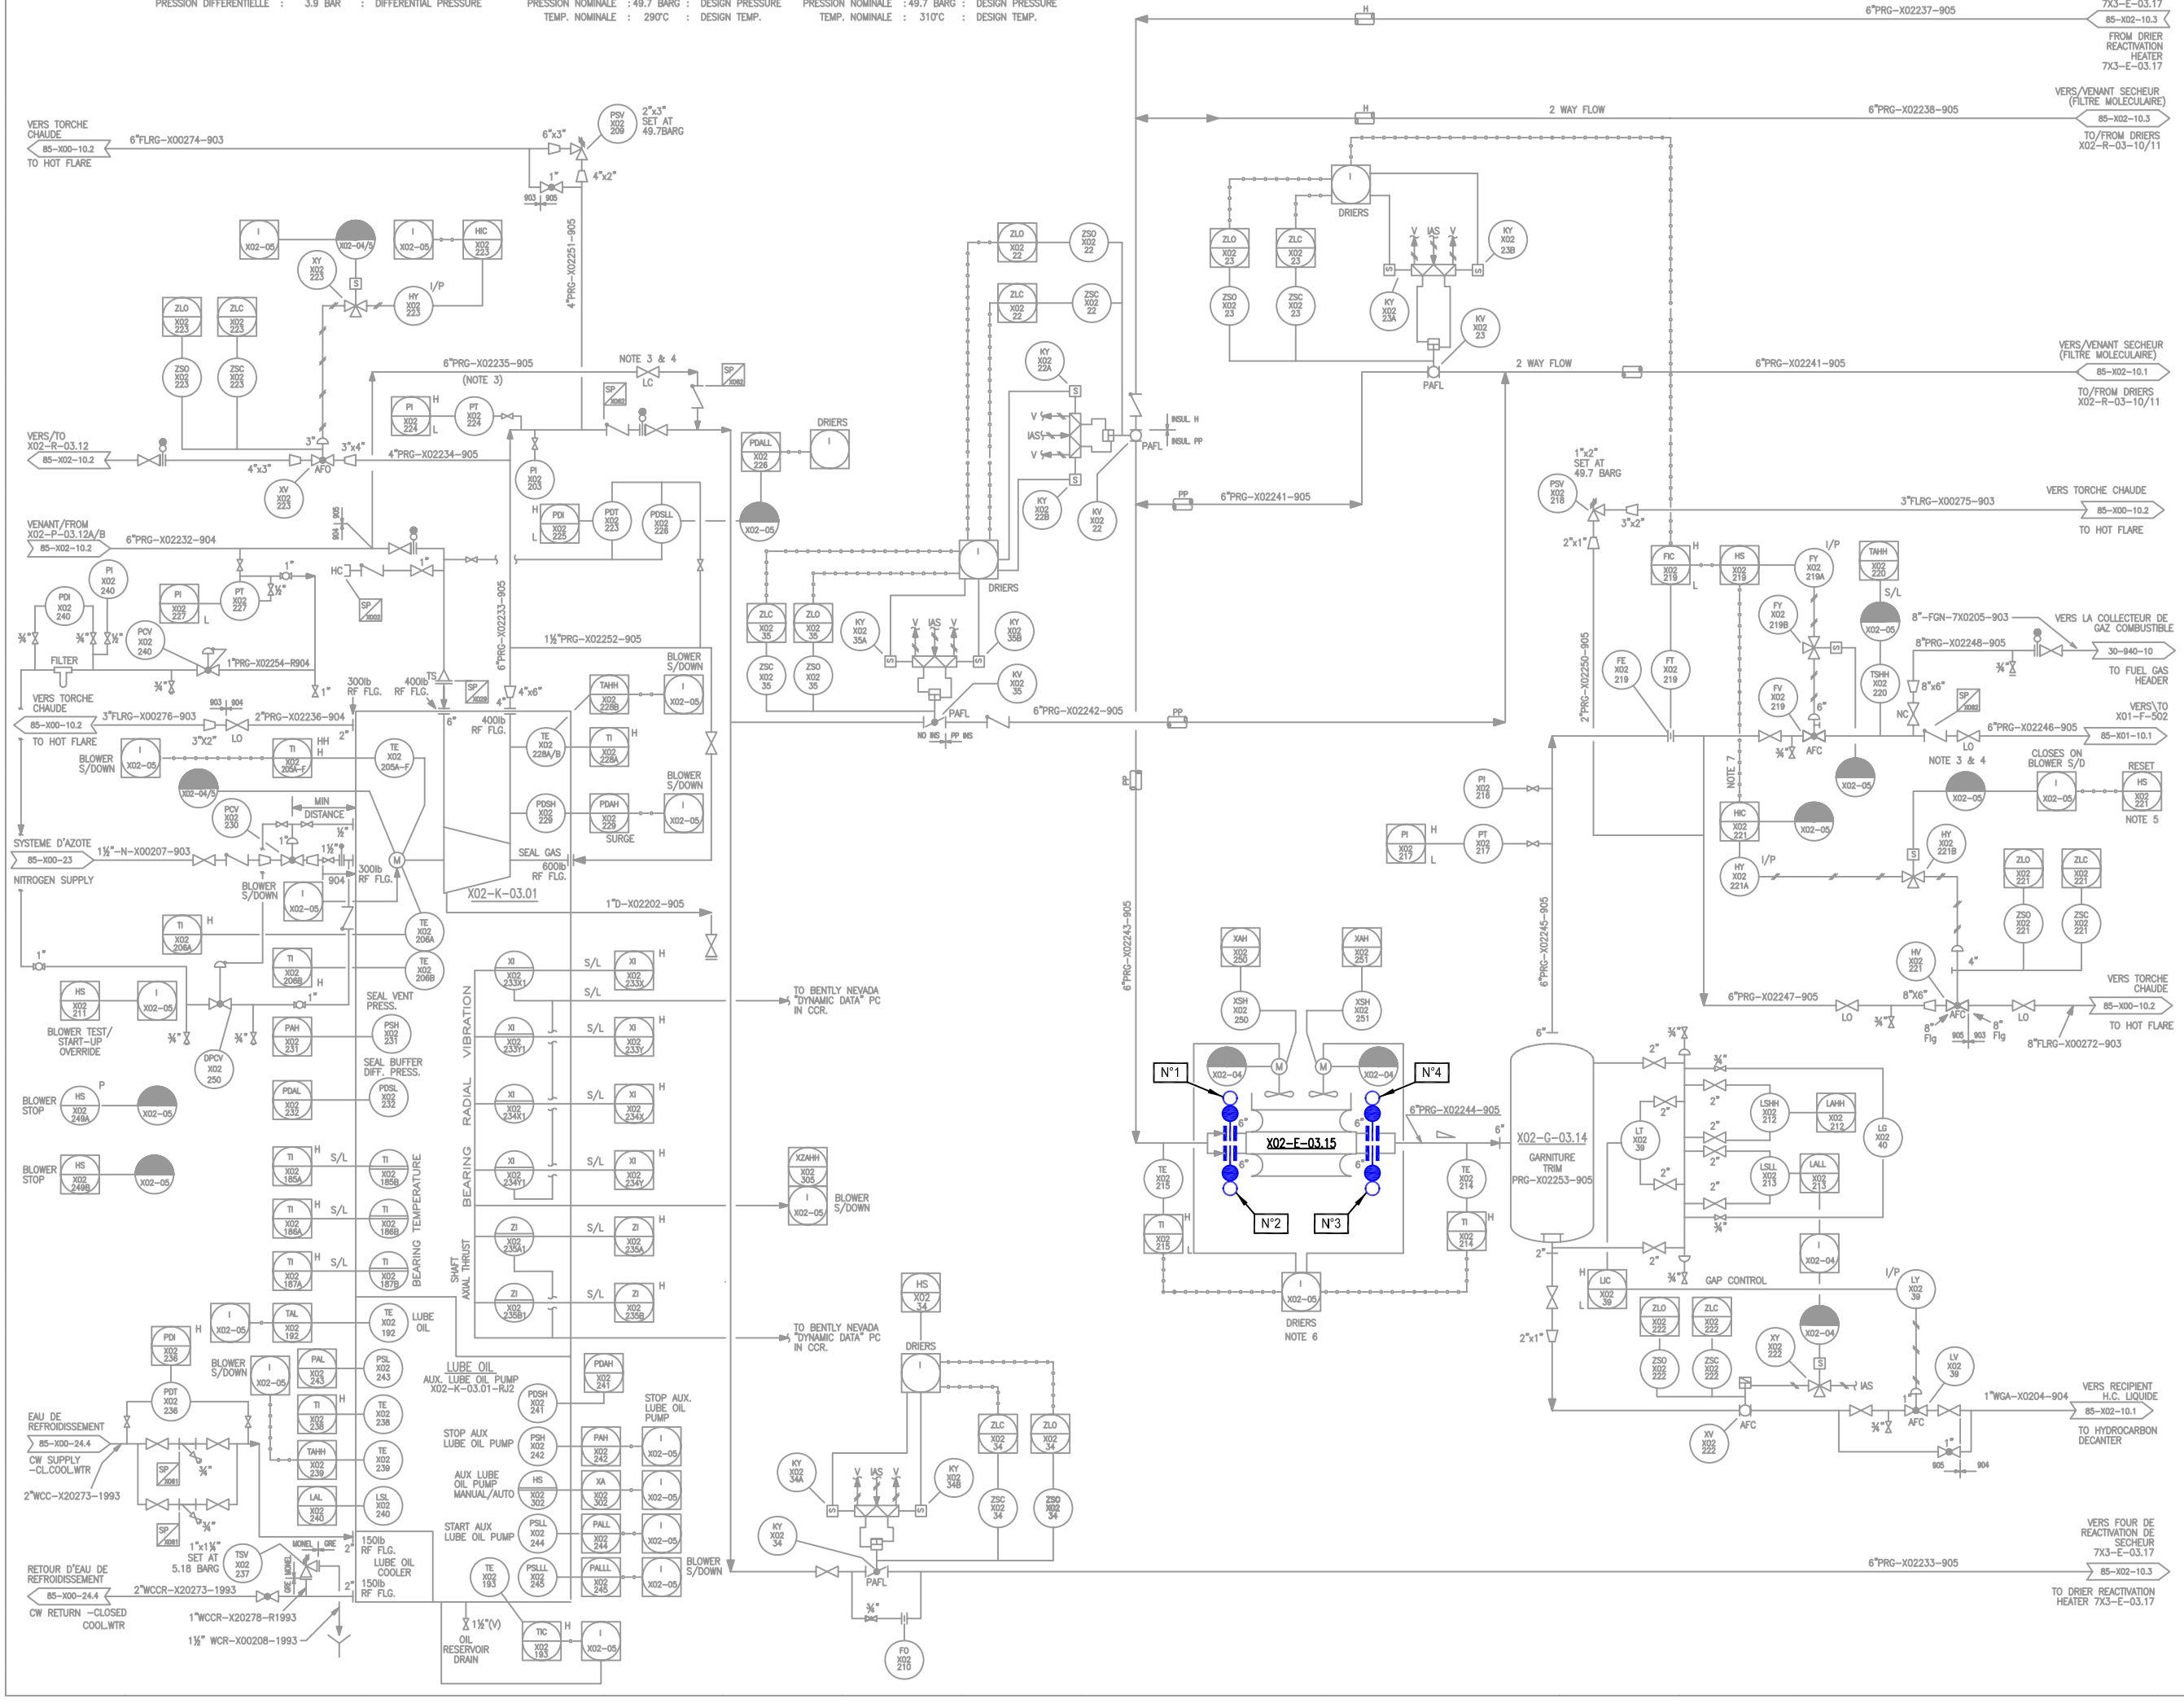

LISTE DES BRIDES D'ISOLEMENT

Brides N°	Localisation du plan de bride	N° de ligne	Spec.	Diam. de la bride	Observation
1	Entrée gaz vers E-03.15	6"PRG-X02243	905	6"	
2	Entrée gaz vers E-03.15	6"PRG-X02243	905	6"	
3	Sortie gaz E-03.15 vers G-03.14	6"PRG-X02244	905	6"	
4	Sortie gaz E-03.15 vers G-03.14	6"PRG-X02244	905	6"	

PLAN DE REFERENCE

P&ID 85-X02-10.4

REV.	DATE	REVISION	BY	CHK	OPTO SUPV	GESTN ENGIN	PROJ MGR	CLIENT
0	15-05-2005	EMIS POUR INSTALLATION	BB					

ECHELLE / SCALE : NONE — ETABLI / DRAWN : B.BOURA — VERIFIE / CHECKED :

S O N A T R A C H
ALGERIE

SONATRACH UNITE DE GNL
RENOVATION COMPLEXE GL1.Z
BETHIOUA, ALGERIE

SONATRACH LNG PLANT
GL1.Z RENOVATION
BETHIOUA, ALGERIA

PROCEDURE DE MISE SOUS JOINT PLEINS DE L'ECHANGEUR X02-E-03.15

JOB N°	DRAWING N°	REV.
T-1087	DS X02-E-03.15	0