## LISTE DES BRIDES D'ISOLEMENT

| Brides N° | Localisation du plan de bride | N° de ligne | Spec. | Diam. de la bride | Observation |
|---|---|---|---|---|---|
| 1 | Sortie E.D.M. | 3"WCR-X0023 | 1082 | 3" | |
| 2 | Entree gasoline vers E-07.53 | 3"G-X1001 | 903 | 3" | |
| 3 | Entree E.D.M. | 3"WC-X00202 | 1993 | 3" | |
| 4 | Sortie gasoline | 2"G-X1002 | 903 | 3" | |

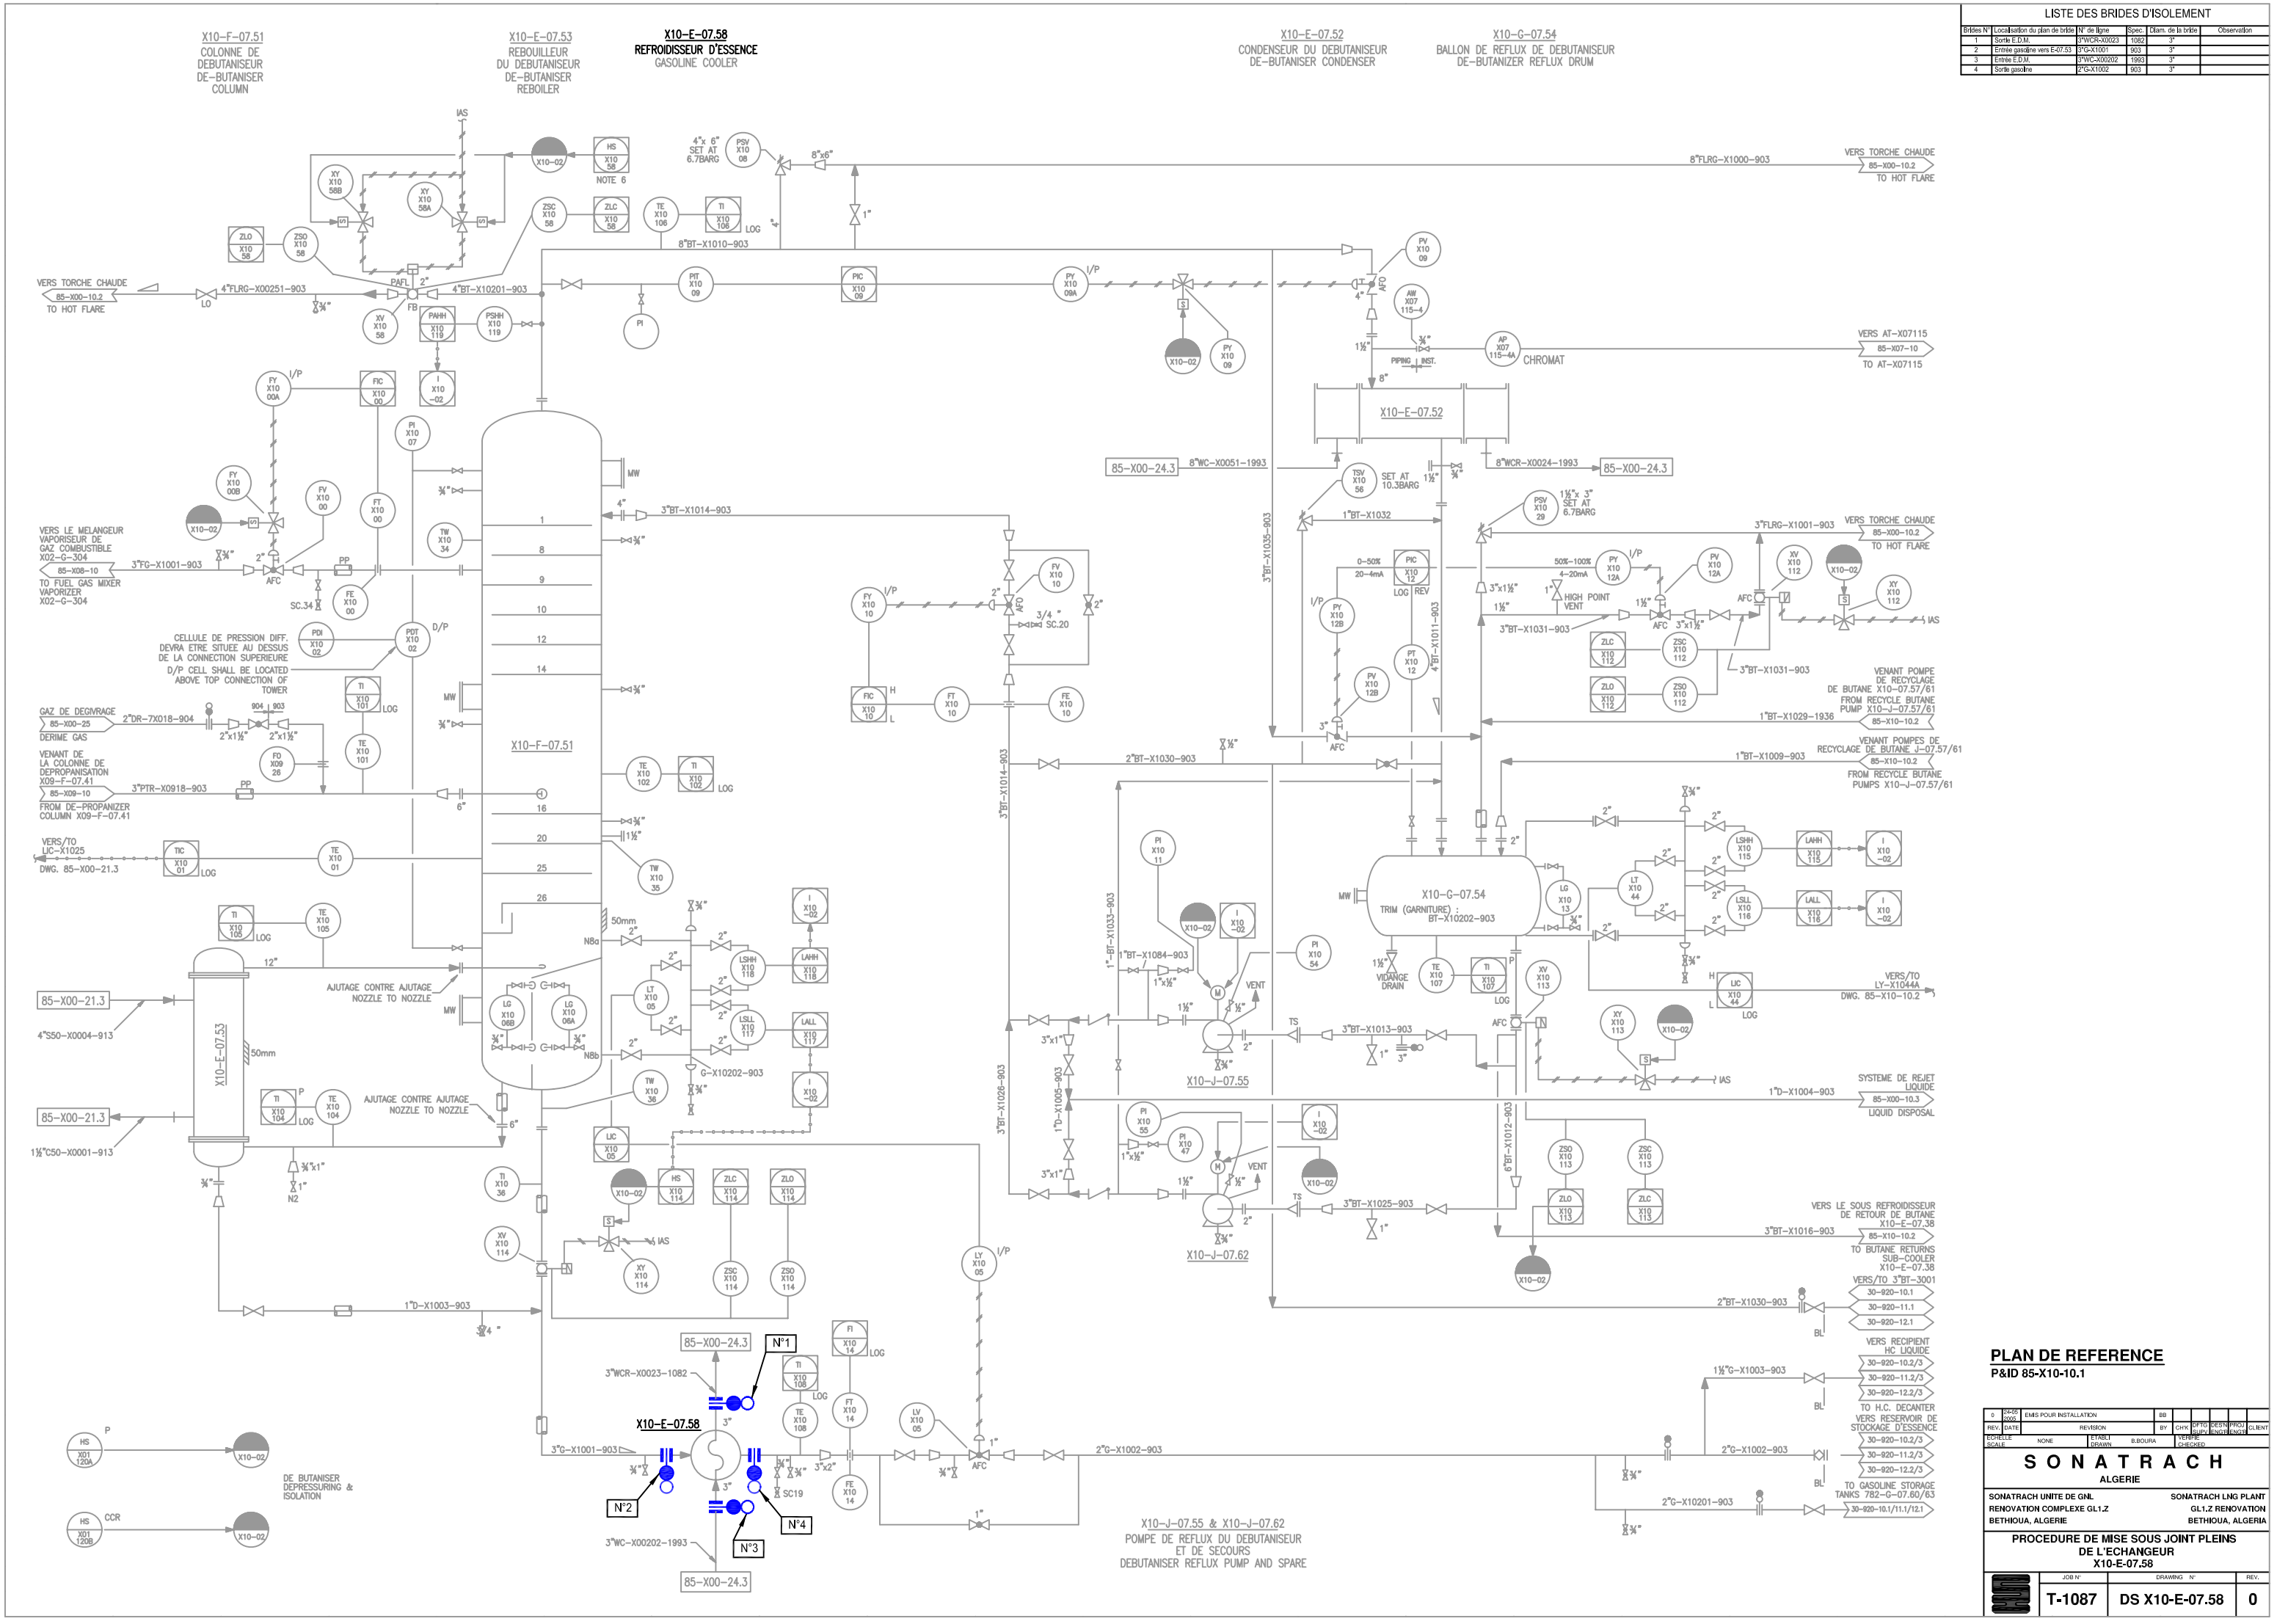


## PLAN DE REFERENCE

P&ID 85-X10-10.1

| REV. | DATE | REVISION | BY | CHK | OPTO SUPV | DESN ENGR | PROJ ENGR | CLIENT |
|---|---|---|---|---|---|---|---|---|
| 0 | 30-05-2005 | EMIS POUR INSTALLATION | BB | | | | | |

ECHELLE / SCALE: NONE — ETABLI / DRAWN: B.BOURA — VERIFIE / CHECKED:

**S O N A T R A C H**
ALGERIE

SONATRACH UNITE DE GNL
RENOVATION COMPLEXE GL1.Z
BETHIOUA, ALGERIE

SONATRACH LNG PLANT
GL1.Z RENOVATION
BETHIOUA, ALGERIA

**PROCEDURE DE MISE SOUS JOINT PLEINS DE L'ECHANGEUR X10-E-07.58**

| JOB N° | DRAWING N° | REV. |
|---|---|---|
| T-1087 | DS X10-E-07.58 | 0 |

# PROCEDURE DE MISE SOUS JOINTS PLEINS DE L'ECHANGEUR (X10-E-07.58) POUR TRAVAUX & INSPECTION

| Bride N° | Localisation du plan de bride | N° de Ligne | Spécification des brides | Dimensions des brides | Observations | P&ID N° |
|---|---|---|---|---|---|---|
| 1 | Sortie E.D.M | 3"WCR-X0023 | 1082 | 3" | | 85-X10-10.1 |
| 2 | Entrée gasoline vers E-07.58 | 3"G-X1001 | 903 | 3" | | 85-X10-10.1 |
| 3 | Entrée E.D.M. | 3"WC-X00202 | 1993 | 3" | | 85-X10-10.1 |
| 4 | Sortie gasoline | 2"G-X1002 | 903 | 3" | | 85-X10-10.1 |

| | DATE | SIGNATURE |
|---|---|---|
| DEPARTEMENT TECHNIQUE | 27/02/13 | |
| DEPARTEMENT PRODUCTION | 28.02.13 | p/ HESTS |