LISTE DES BRIDES D'ISOLEMENT

Brides N°	Localisation du plan de bride	N° de ligne	Spec.	Diam. de la bride	Observation
1	Entrée gaz vers E-506	20"PRG-X0111	904	20"	
2	Sortie condensat	3"CS0-X0016	913	3"	
3	Sortie gaz vers F-502	20"PRG-X0112	904	20"	
4	Entrée vapeur vers E-506	6"S50-X0015	913	6"	

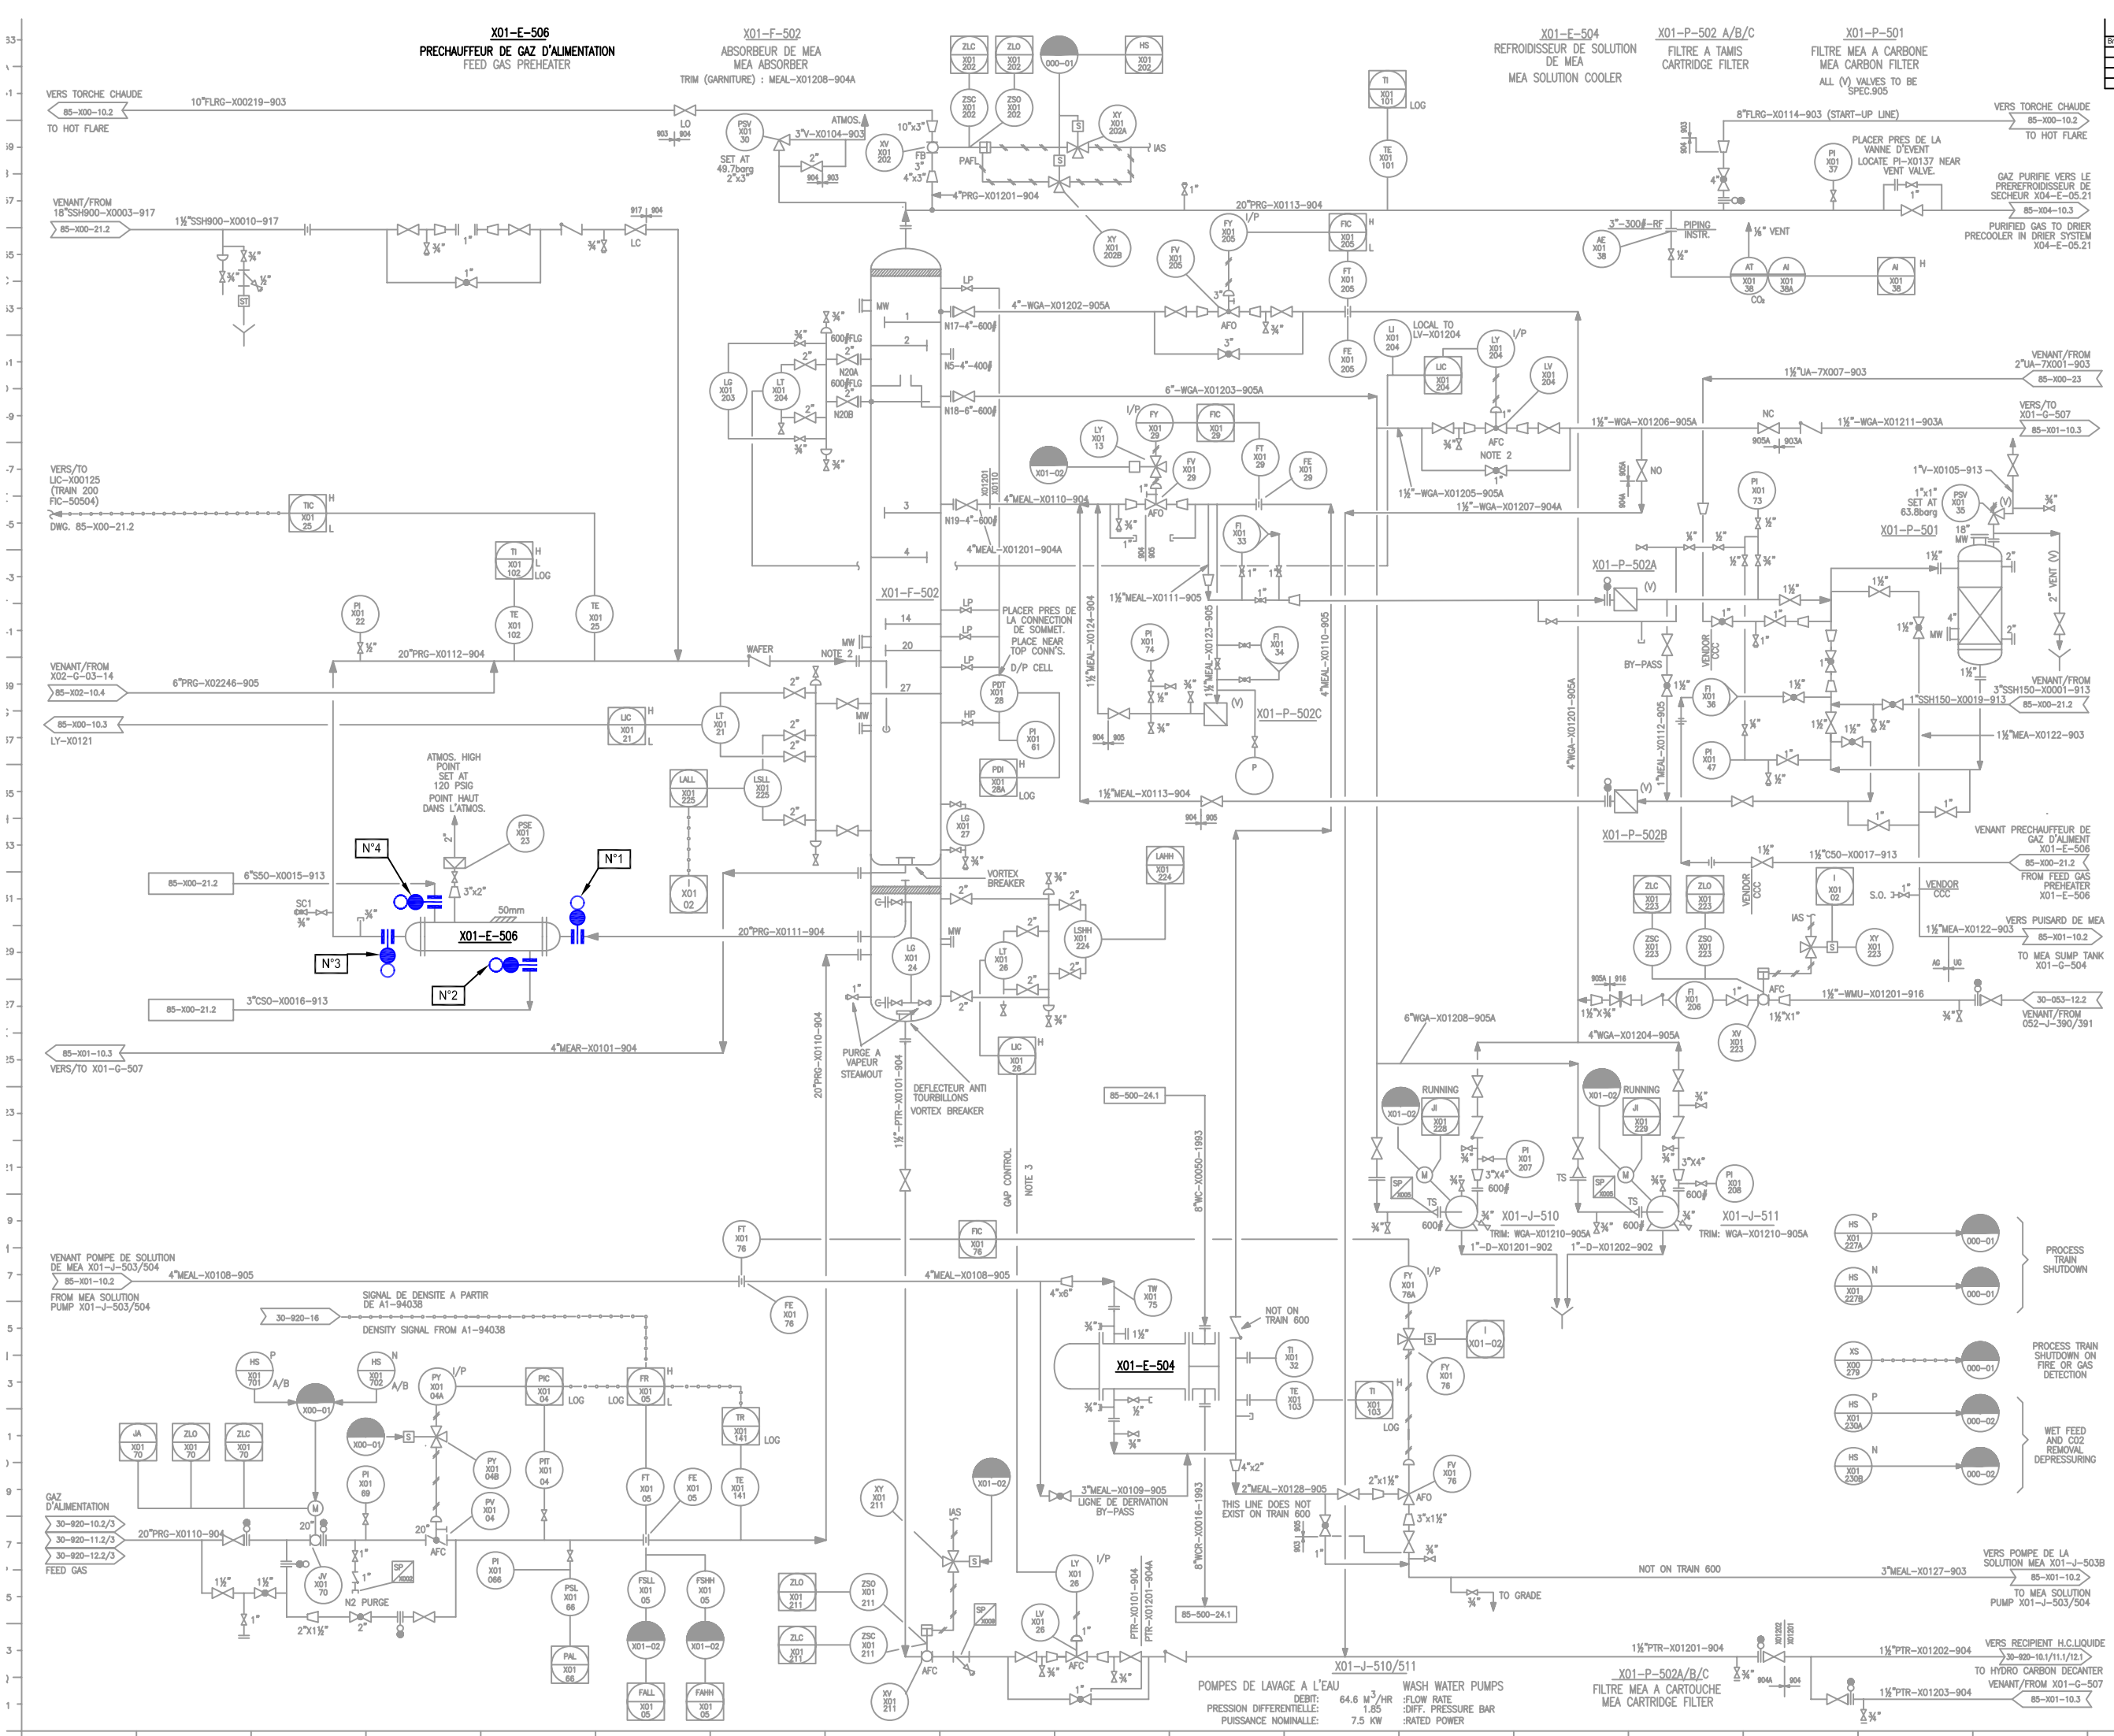

PLAN DE REFERENCE

P&ID 85-X01-10.1

REV.	DATE	REVISION	BY	CHK	OPTO	DESN	PROJ	CLIEN
0	25-05-2005	EMIS POUR INSTALLATION	SB					

ECHELLE / SCALE: NONE — EYABLI / DRAWN: B.BOURA — VERIFIE / CHECKED

S O N A T R A C H
ALGERIE

SONATRACH UNITE DE GNL
RENOVATION COMPLEXE GL1,Z
BETHIOUA, ALGERIE

SONATRACH LNG PLANT
GL1,Z RENOVATION
BETHIOUA, ALGERIA

PROCEDURE DE MISE SOUS JOINT PLEINS DE L'ECHANGEUR XO1-E-506

JOB N°	DRAWING N°	REV.
T-1087	DS X01-E-506	0

PROCEDURE DE MISE SOUS JOINTS PLEINS DE L'ECHANGEUR (X01-E-506) POUR TRAVAUX & INSPECTION

Bride N°	Localisation du plan de bride	N° de Ligne	Spécification des brides	Dimensions des brides	Epaisseurs des brides (mm)	Observations	P&ID N°
1	Sortie gaz vers E-506	20"PRG-X0111	904	20"			DS X01-E-506 Rév 0
2	Sortie condensât	3"C50-X0016	913	3"			DS X01-E-506 Rév 0
3	Sortie gaz vers F-502	20"PRG-X0112	904	20"			DS X01-E-506 Rév 0
4	Entrée vapeur vers E-506	6"S50-X0015	913	6"			DS X01-E-506 Rév 0

	DATE	SIGNATURE
DEPARTEMENT TECHNIQUE	09/04/2012	
DEPARTEMENT PRODUCTION	23/04/2012	