X01-E-505
PURIFICATEUR DE MEA
MEA PURIFIER

X01-E-503 A&B
ECHANGEUR DE SOLUTION DE MEA
MEA SOLUTION EXCHANGER

X01-R-503
SYSTEME D'INJECTION D'INHIBITEUR DE CORROSION
CORROSION INHIBITOR INJECTION PACKAGE

X01-F-501
REGENERATEUR DE MEA
MEA REGENERATOR

X01-E-501
CONDENSEUR DE TETE
OVERHEAD CONDENSER

X01-E-502
REBOUILLEUR DE MEA
MEA REBOILER

X01-G-502
SEPARATEUR ACIDE/GAZ
ACID/GAS SEPARATOR

X01-R-502
SYSTEME D'INJECTION ANTI-MOUSSE
ANTIFOAM INJECTION SYSTEM

X01-R-503J
POMPE INHIBITEUR DE CORROSION
DEBIT: EN INSTANCE
PRESSION DIFFERENTIELLE: EN INSTANCE
PUISSANCE NOMINALLE: EN INSTANCE

CORROSION INHIBITOR PUMP
FLOW RATE: 0.02 M³/HR (MAX)
DIFF. HEAD: 6.74 BAR
RATED POWER: 0.2 KW

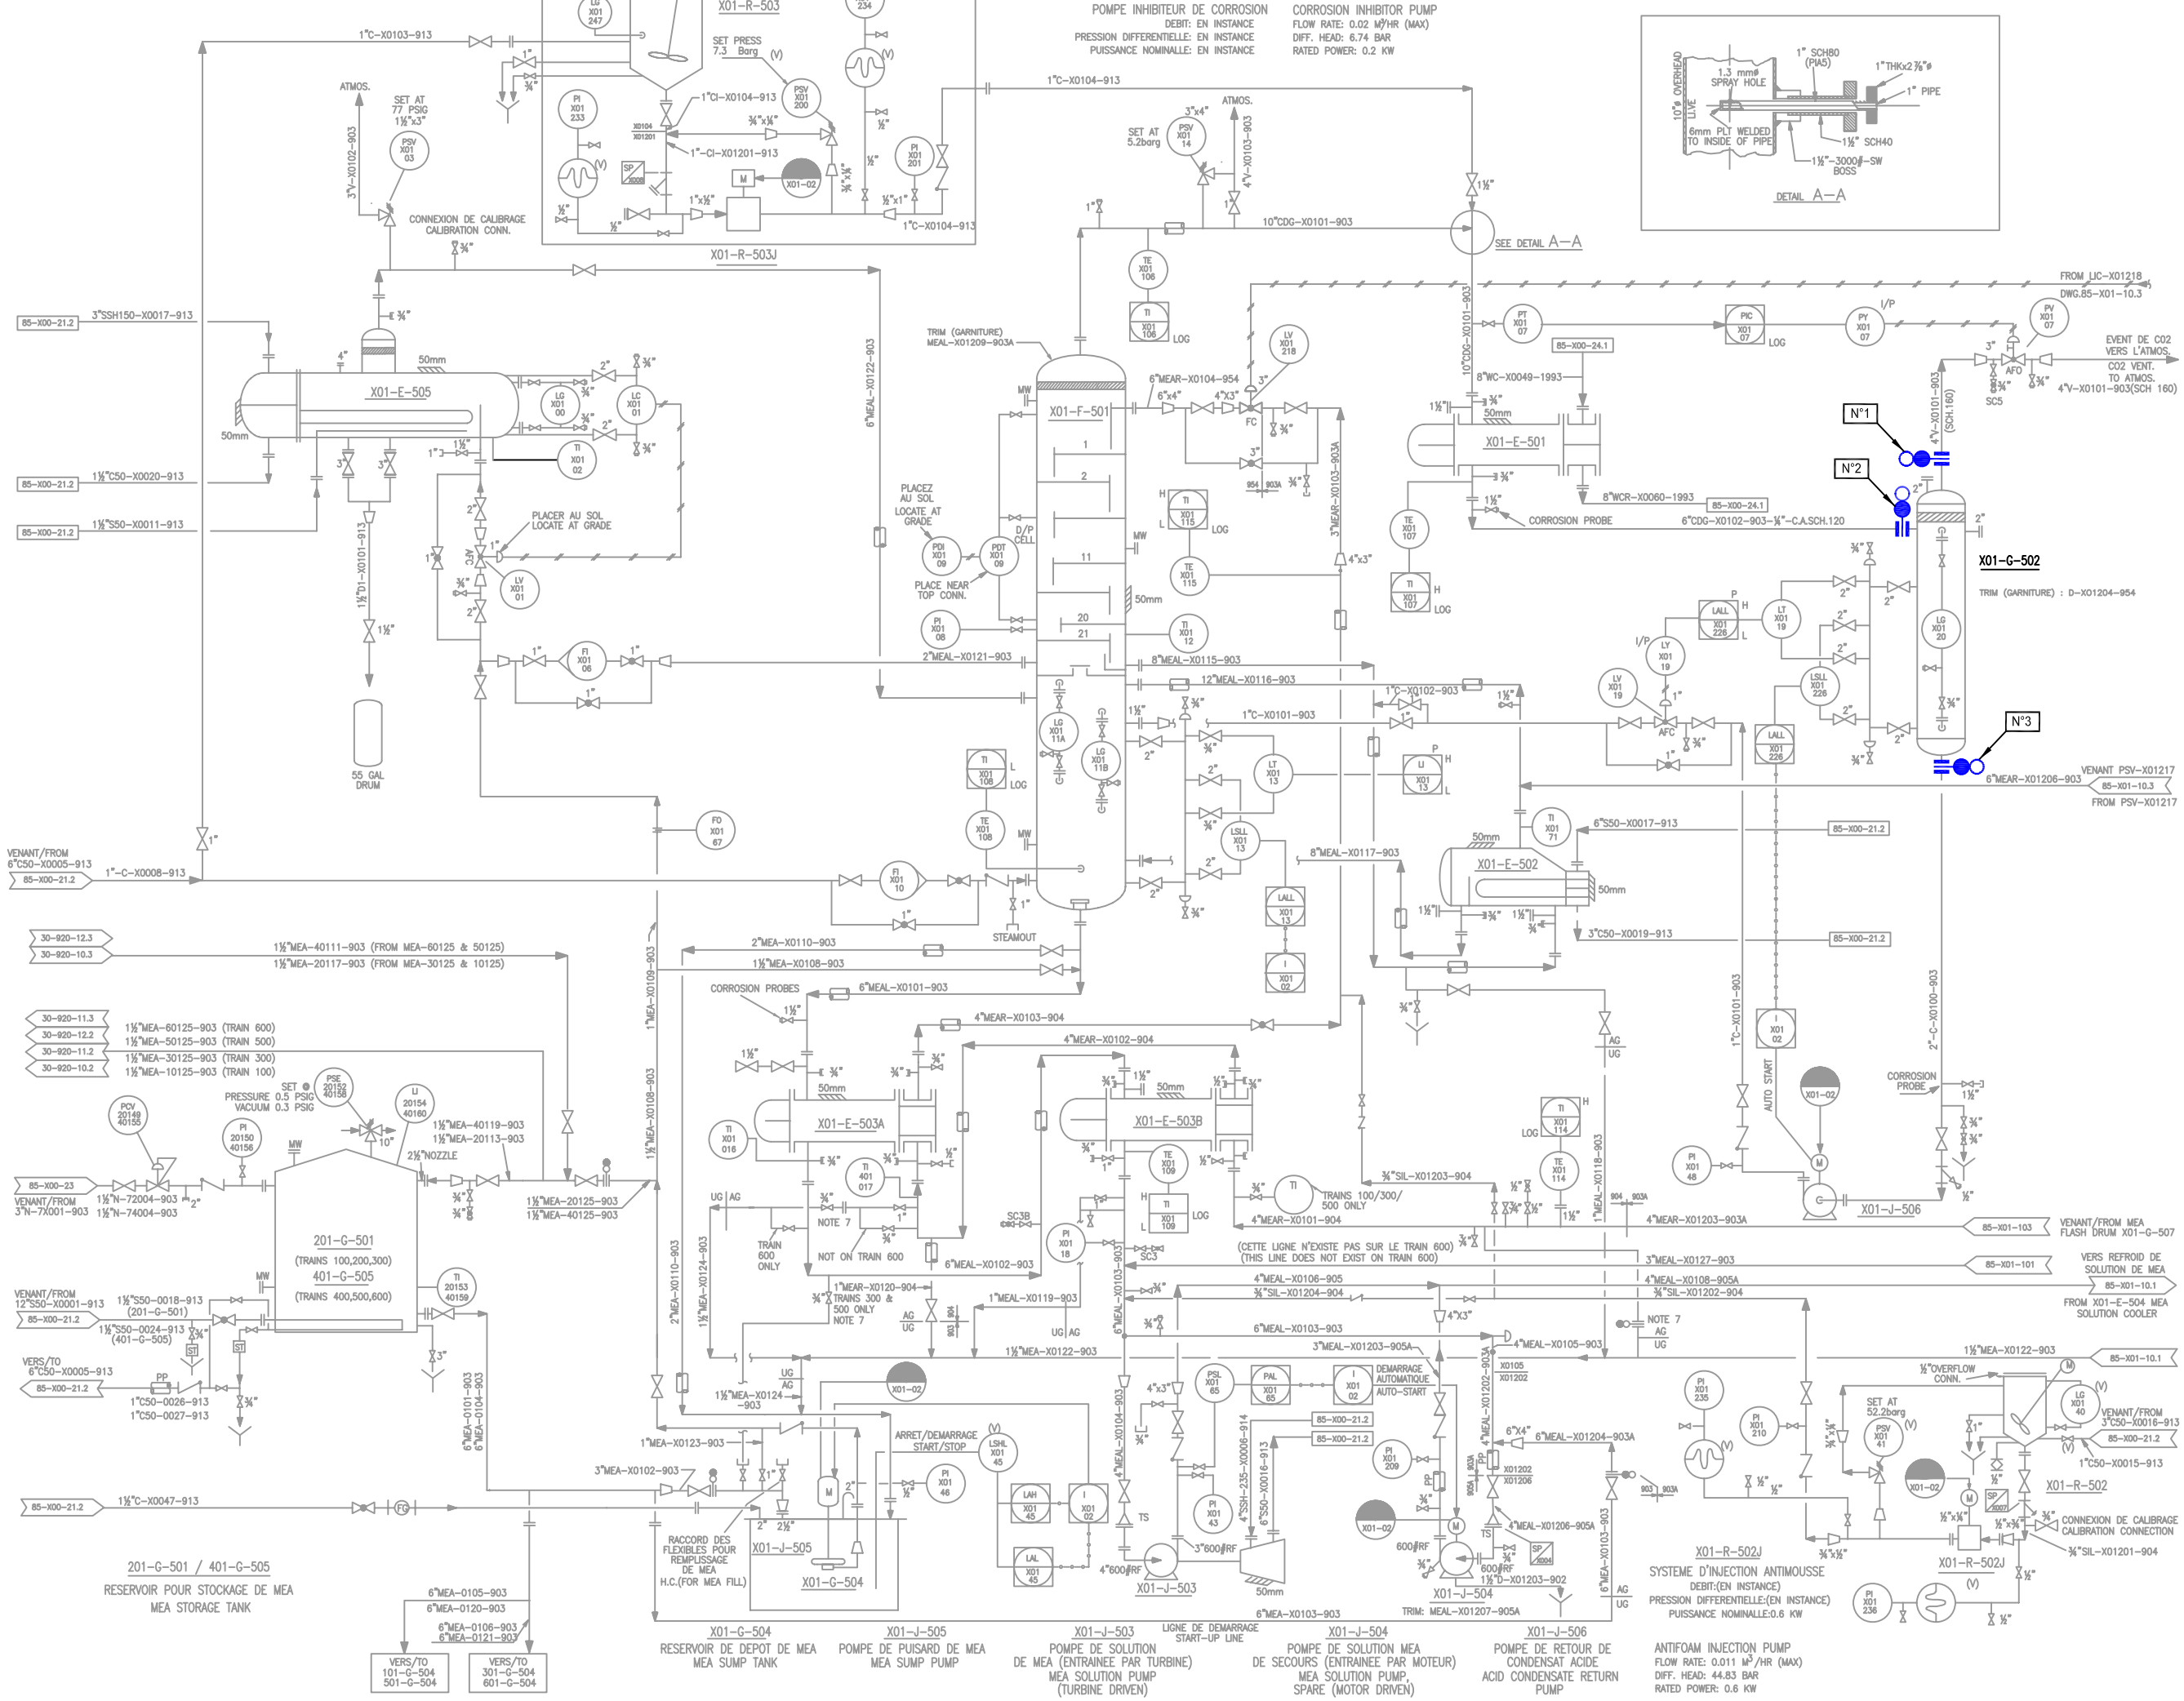

LISTE DES BRIDES D'ISOLEMENT

Brides N°	Localisation du plan de bride	N° de ligne	Spec.	Diam. de la bride	Observation
1	Ligne d'event	4"V–X01101	903	4"	
2	Entrée ligne CDG vers G-502	6"CDG–X01102	904	6"	
3	Sortie condensat vers J-506	2"C–X01100	903	2"	

PLAN DE REFERENCE
P&ID 85-X01-10.2

REV.	DATE	REVISION	BY	CHK	OPTG SUPV	DESN ENGR	PROJ ENGR	CLIENT
0	29-05 2002	EMIS POUR INSTALLATION	BB					

ECHELLE SCALE: NONE | ETABLI DRAWN: B.BOURA | VERIFIE CHECKED:

S O N A T R A C H
ALGERIE

SONATRACH UNITE DE GNL
RENOVATION COMPLEXE GL1.Z
BETHIOUA, ALGERIE

SONATRACH LNG PLANT
GL1.Z RENOVATION
BETHIOUA, ALGERIA

PROCEDURE DE MISE SOUS JOINT PLEINS DE SEPARATEUR ACIDE / GAZ XO1-G-502

JOB N°	DRAWING N°	REV.
T-1087	DS X01-G-502	0

PROCEDURE DE MISE SOUS JOINTS PLEINS DE SEPARATEUR ACIDE / GAZ (X01-G-502) POUR TRAVAUX & INSPECTION

Bride N°	Localisation du plan de bride	N° de Ligne	Spécification des brides	Dimensions des brides	Epaisseurs des brides	Observations	P&ID N°
1	Ligne d'évent	4"V-X0101	903	4"			DS X01-G-502 Rév 0
2	Entrée ligne CDG vers G-502	6"CDG-X0102	903	6"			DS X01-G-502 Rév 0
3	Sortie condensât vers J-506	2"C-X0100	903	2"			DS X01-G-502 Rév 0

	DATE	SIGNATURE
DEPARTEMENT TECHNIQUE	09/04/2012	
DEPARTEMENT PRODUCTION	27/04/2012	