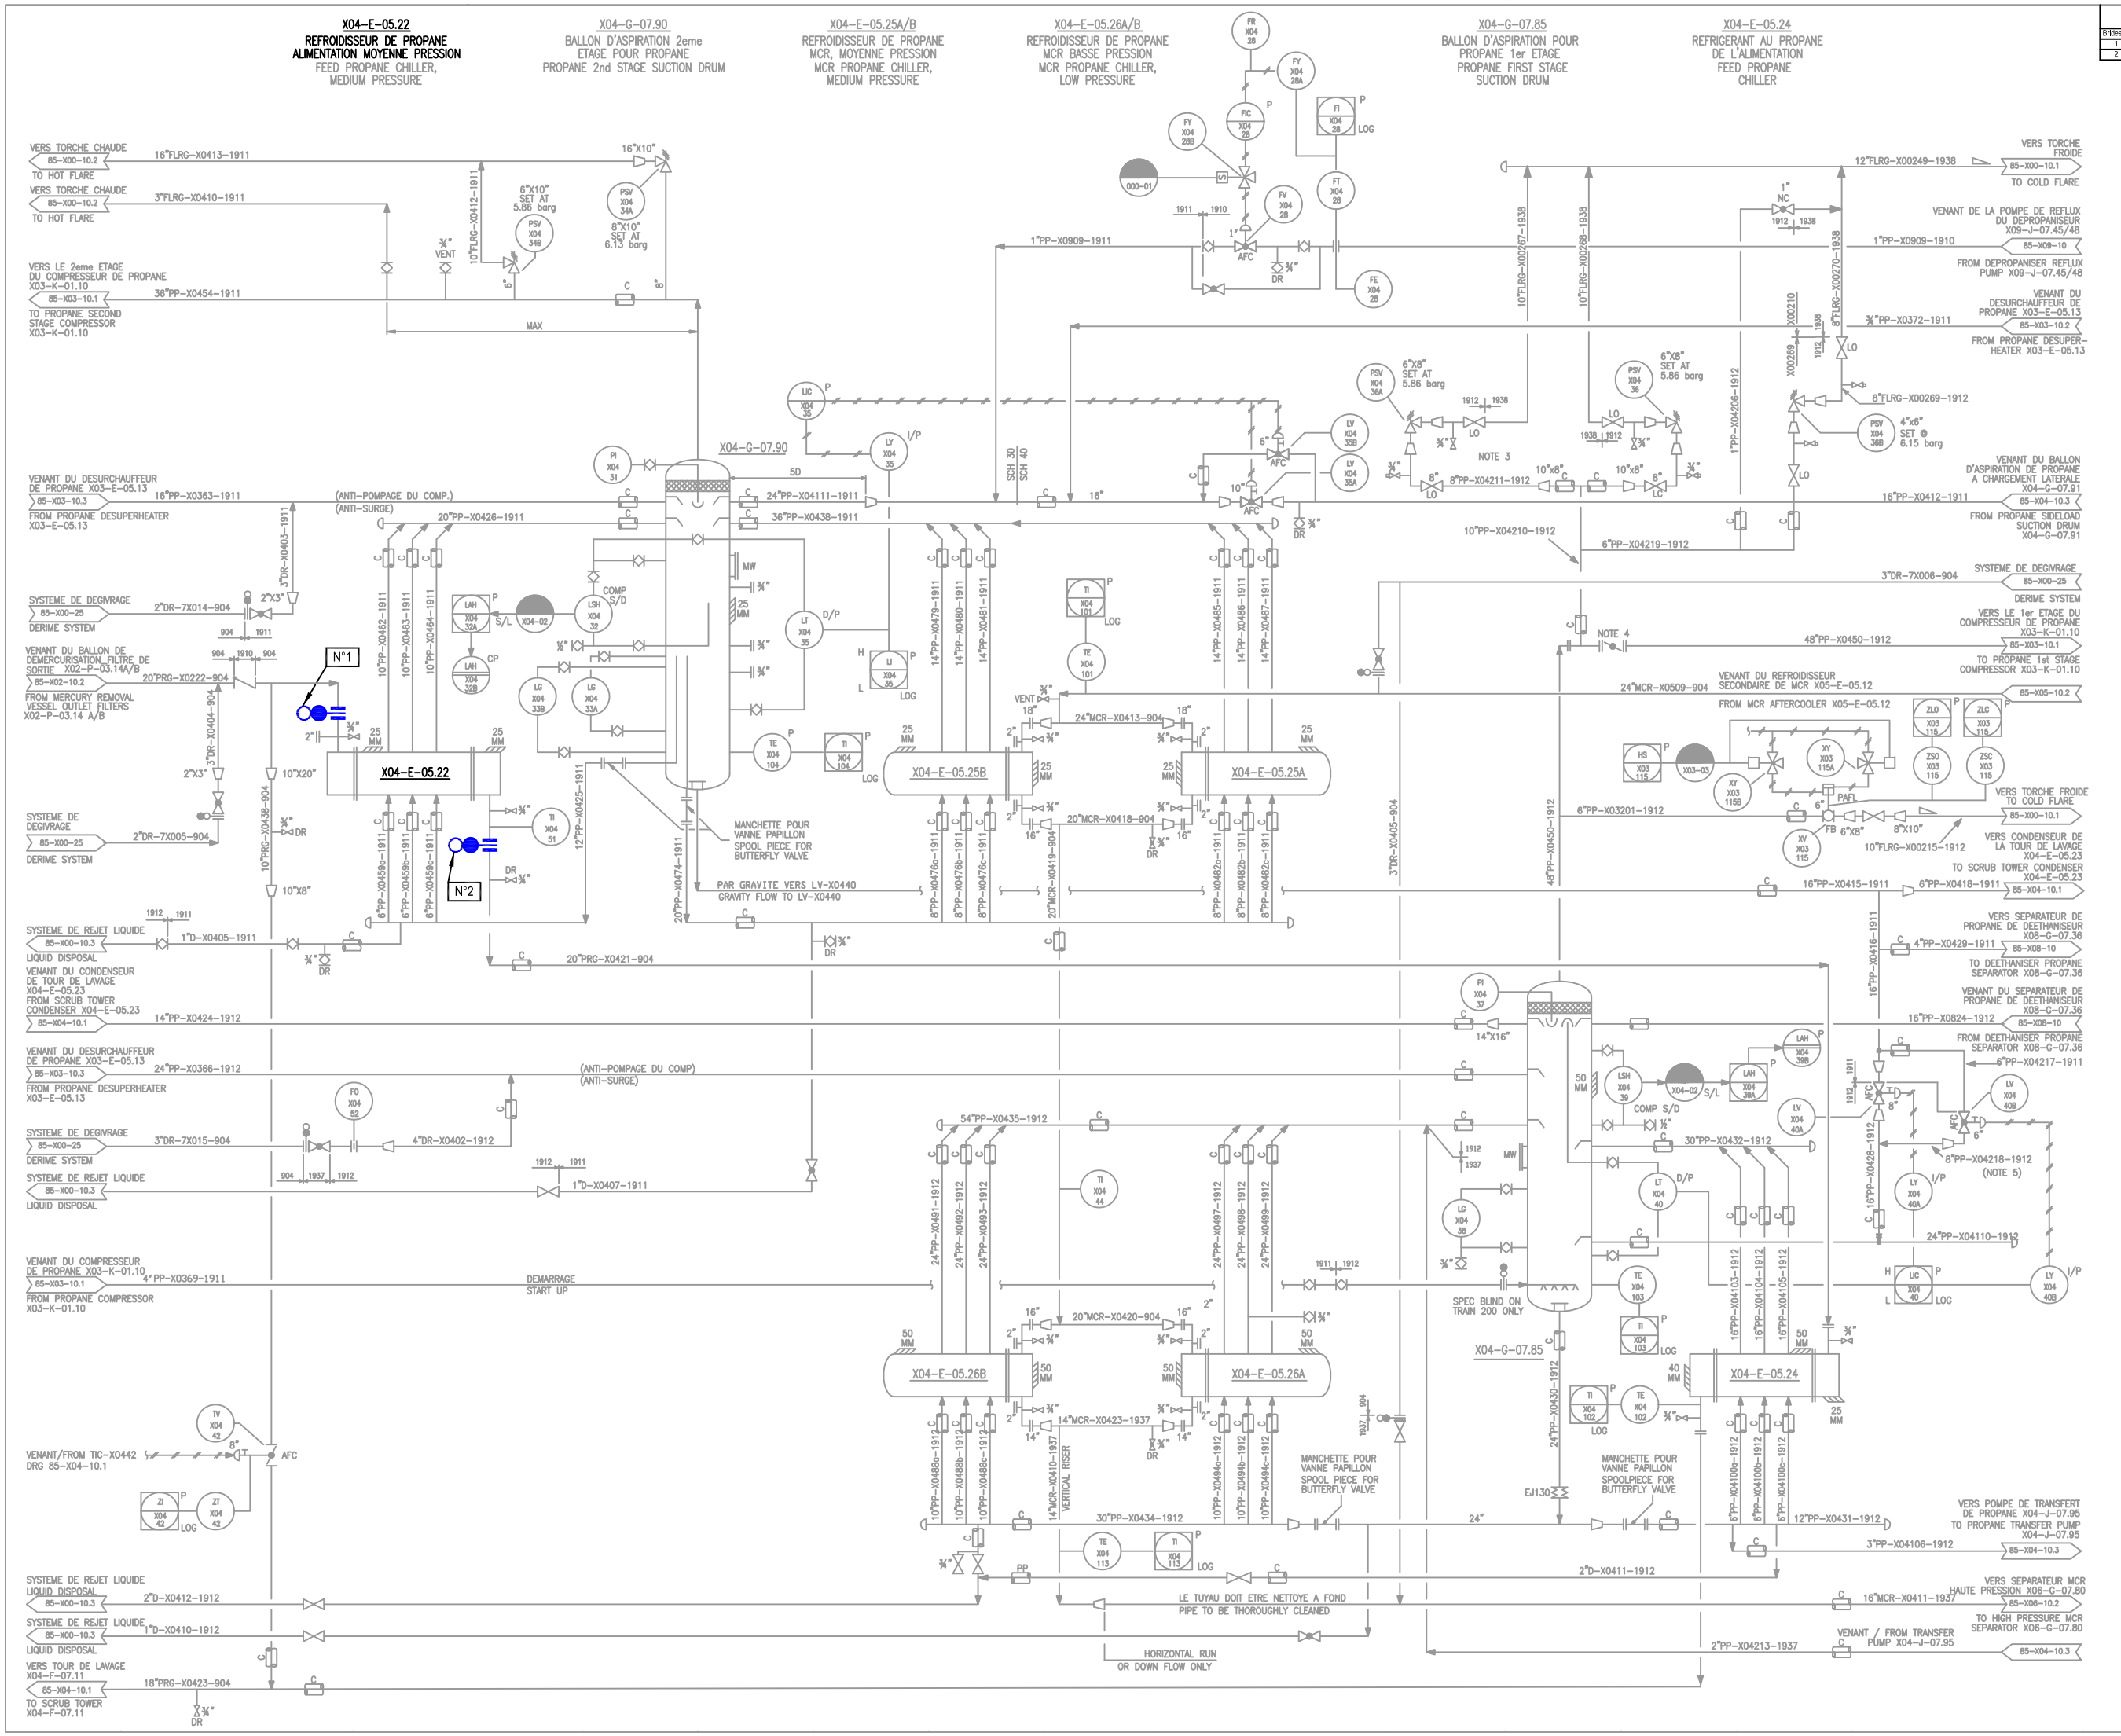

LISTE DES BRIDES D'ISOLEMENT

Brides N°	Localisation du plan de bride	N° de ligne	Spec.	Diam. de la bride	Observation
1	Entrée gaz venant du P-03.14A/B	20"PRG-X0222	904	20"	
2	Sortie gaz vers E-05.24	20"PRG-X0421	904	20"	

PROCEDURE DE MISE SOUS JOINTS PLEINS DE L'ECHANGEUR (X04-E-05.22) POUR TRAVAUX & INSPECTION

Bride N°	Localisation du plan de bride	N° de Ligne	Spécification des brides	Dimensions des brides	Observations	P&ID N°
1	Entrée gaz venant du P-03.14A/B vers E-05.24	20''PRG-X0222	904	20''		85-X04-10.2
2	Sortie gaz vers E-05.24	20''PRG-X0421	904	20''		85-X04-10.2

	DATE	SIGNATURE
DEPARTEMENT TECHNIQUE	05/05/2014	
DEPARTEMENT PRODUCTION	10/06/14	