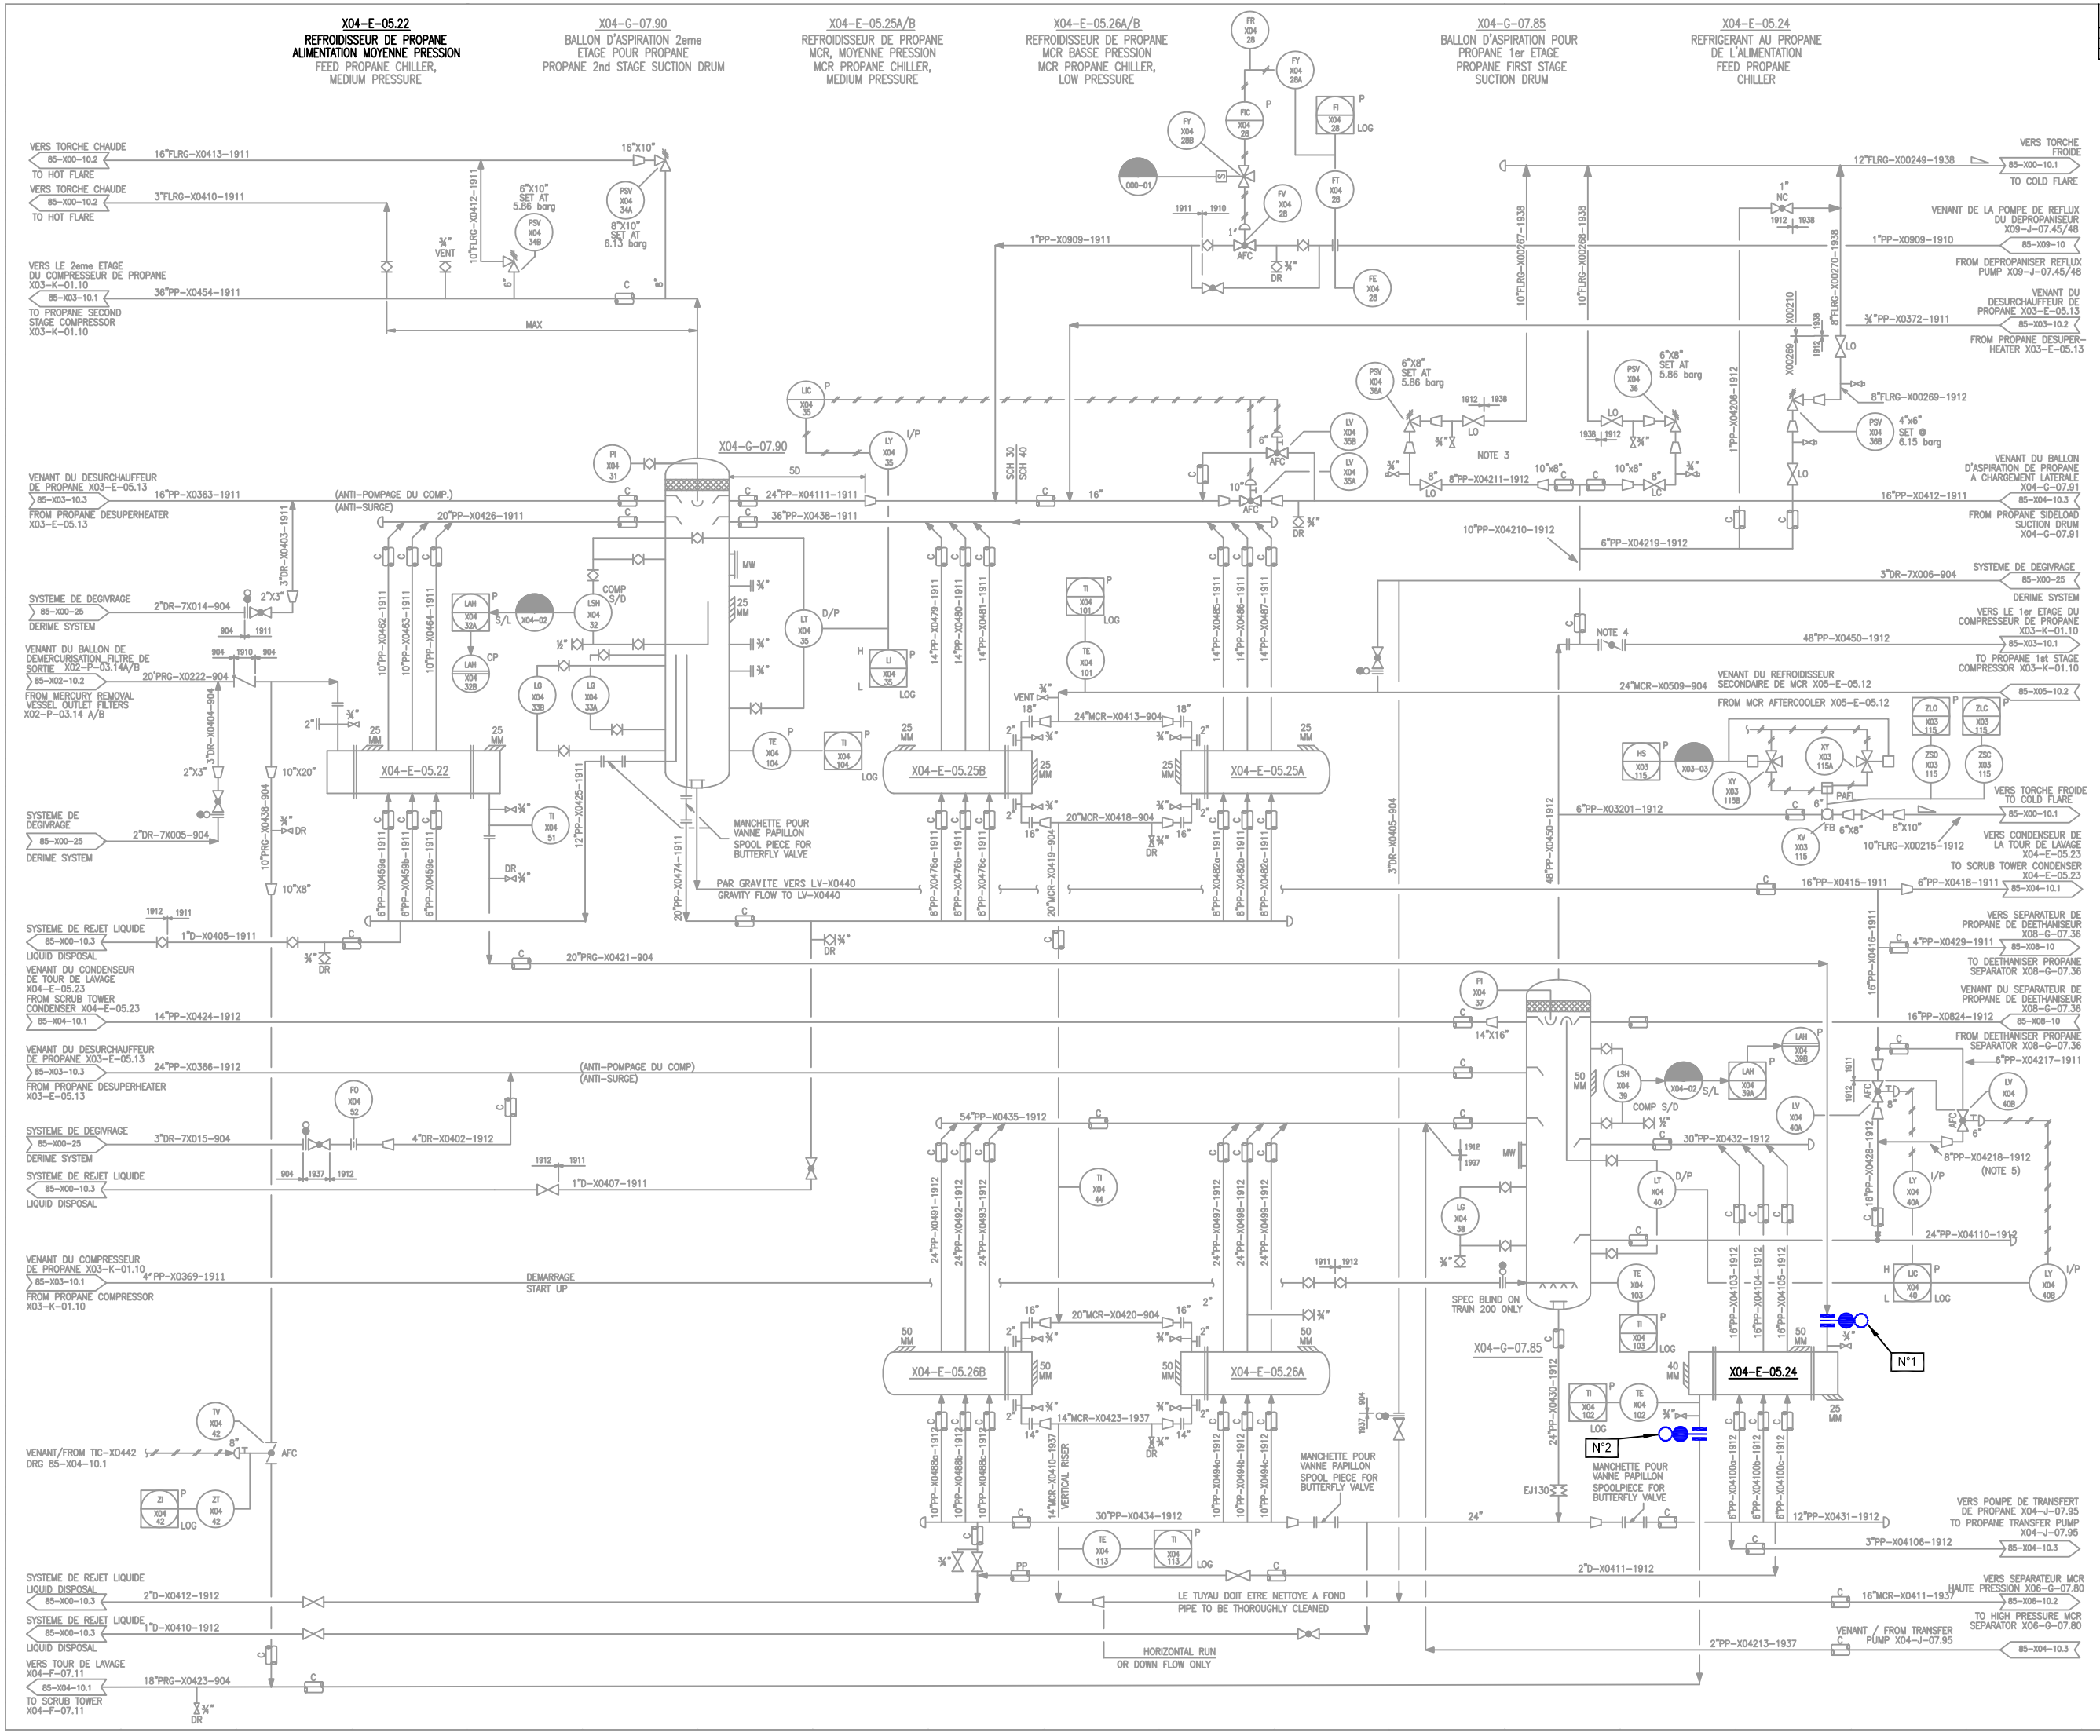

LISTE DES BRIDES D'ISOLEMENT

Brides N°	Localisation du plan de bride	N° de ligne	Spec.	Diam. de la bride	Observation
1	Entrée gaz vers E-05.22	20"PRG-X0421	904	20"	
2	Sortie gaz vers F-07.11	18"PRG-X0423	904	18"	

PLAN DE REFERENCE

P&ID 85-X04-10.2

REV.	DATE	REVISION	BY	CHK	GPTO SUPV	DESN ENGR	PROJ ENGR	CLIENT
0	16-05-2005	EMIS POUR INSTALLATION	BB					

ECHELLE / SCALE: NONE — ETABLI / DRAWN: B.BOURA — VERIFIE / CHECKED:

S O N A T R A C H
ALGERIE

SONATRACH UNITE DE GNL
RENOVATION COMPLEXE GL1.Z
BETHIOUA, ALGERIE

SONATRACH LNG PLANT
GL1.Z RENOVATION
BETHIOUA, ALGERIA

PROCEDURE DE MISE SOUS JOINT PLEINS DE L'ECHANGEUR XO4-E-05.24

JOB N°	DRAWING N°	REV.
T-1087	DS X04-E-05.24	0

PROCEDURE DE MISE SOUS JOINTS PLEINS DE L'ECHANGEUR (X04-E-05.24) POUR TRAVAUX & INSPECTION

Bride N°	Localisation du plan de bride	N° de Ligne	Spécification des brides	Dimensions des brides	Observations	P&ID N°
1	Venant de l'E-05.22	20''PRG-X0421	904	20''		85-X04-10.2
2	Sortie gaz vers F-07.21	18''PRG-X0423	904	18''		85-X04-10.2

NB : pour le bridage coté calandre, le bridage du ballon G-785 est déjà bridé.

	DATE	SIGNATURE
DEPARTEMENT TECHNIQUE	13/05/2014	
DEPARTEMENT PRODUCTION	14.05.14	