X04-E-05.22
REFROIDISSEUR DE PROPANE
ALIMENTATION MOYENNE PRESSION
FEED PROPANE CHILLER,
MEDIUM PRESSURE

X04-G-07.90
BALLON D'ASPIRATION 2eme
ETAGE POUR PROPANE
PROPANE 2nd STAGE SUCTION DRUM

X04-E-05.25A/B
REFROIDISSEUR DE PROPANE
MCR, MOYENNE PRESSION
MCR PROPANE CHILLER,
MEDIUM PRESSURE

X04-E-05.26A/B
REFROIDISSEUR DE PROPANE
MCR BASSE PRESSION
MCR PROPANE CHILLER,
LOW PRESSURE

X04-G-07.85
BALLON D'ASPIRATION POUR
PROPANE 1er ETAGE
PROPANE FIRST STAGE
SUCTION DRUM

X04-E-05.24
REFRIGERANT AU PROPANE
DE L'ALIMENTATION
FEED PROPANE
CHILLER

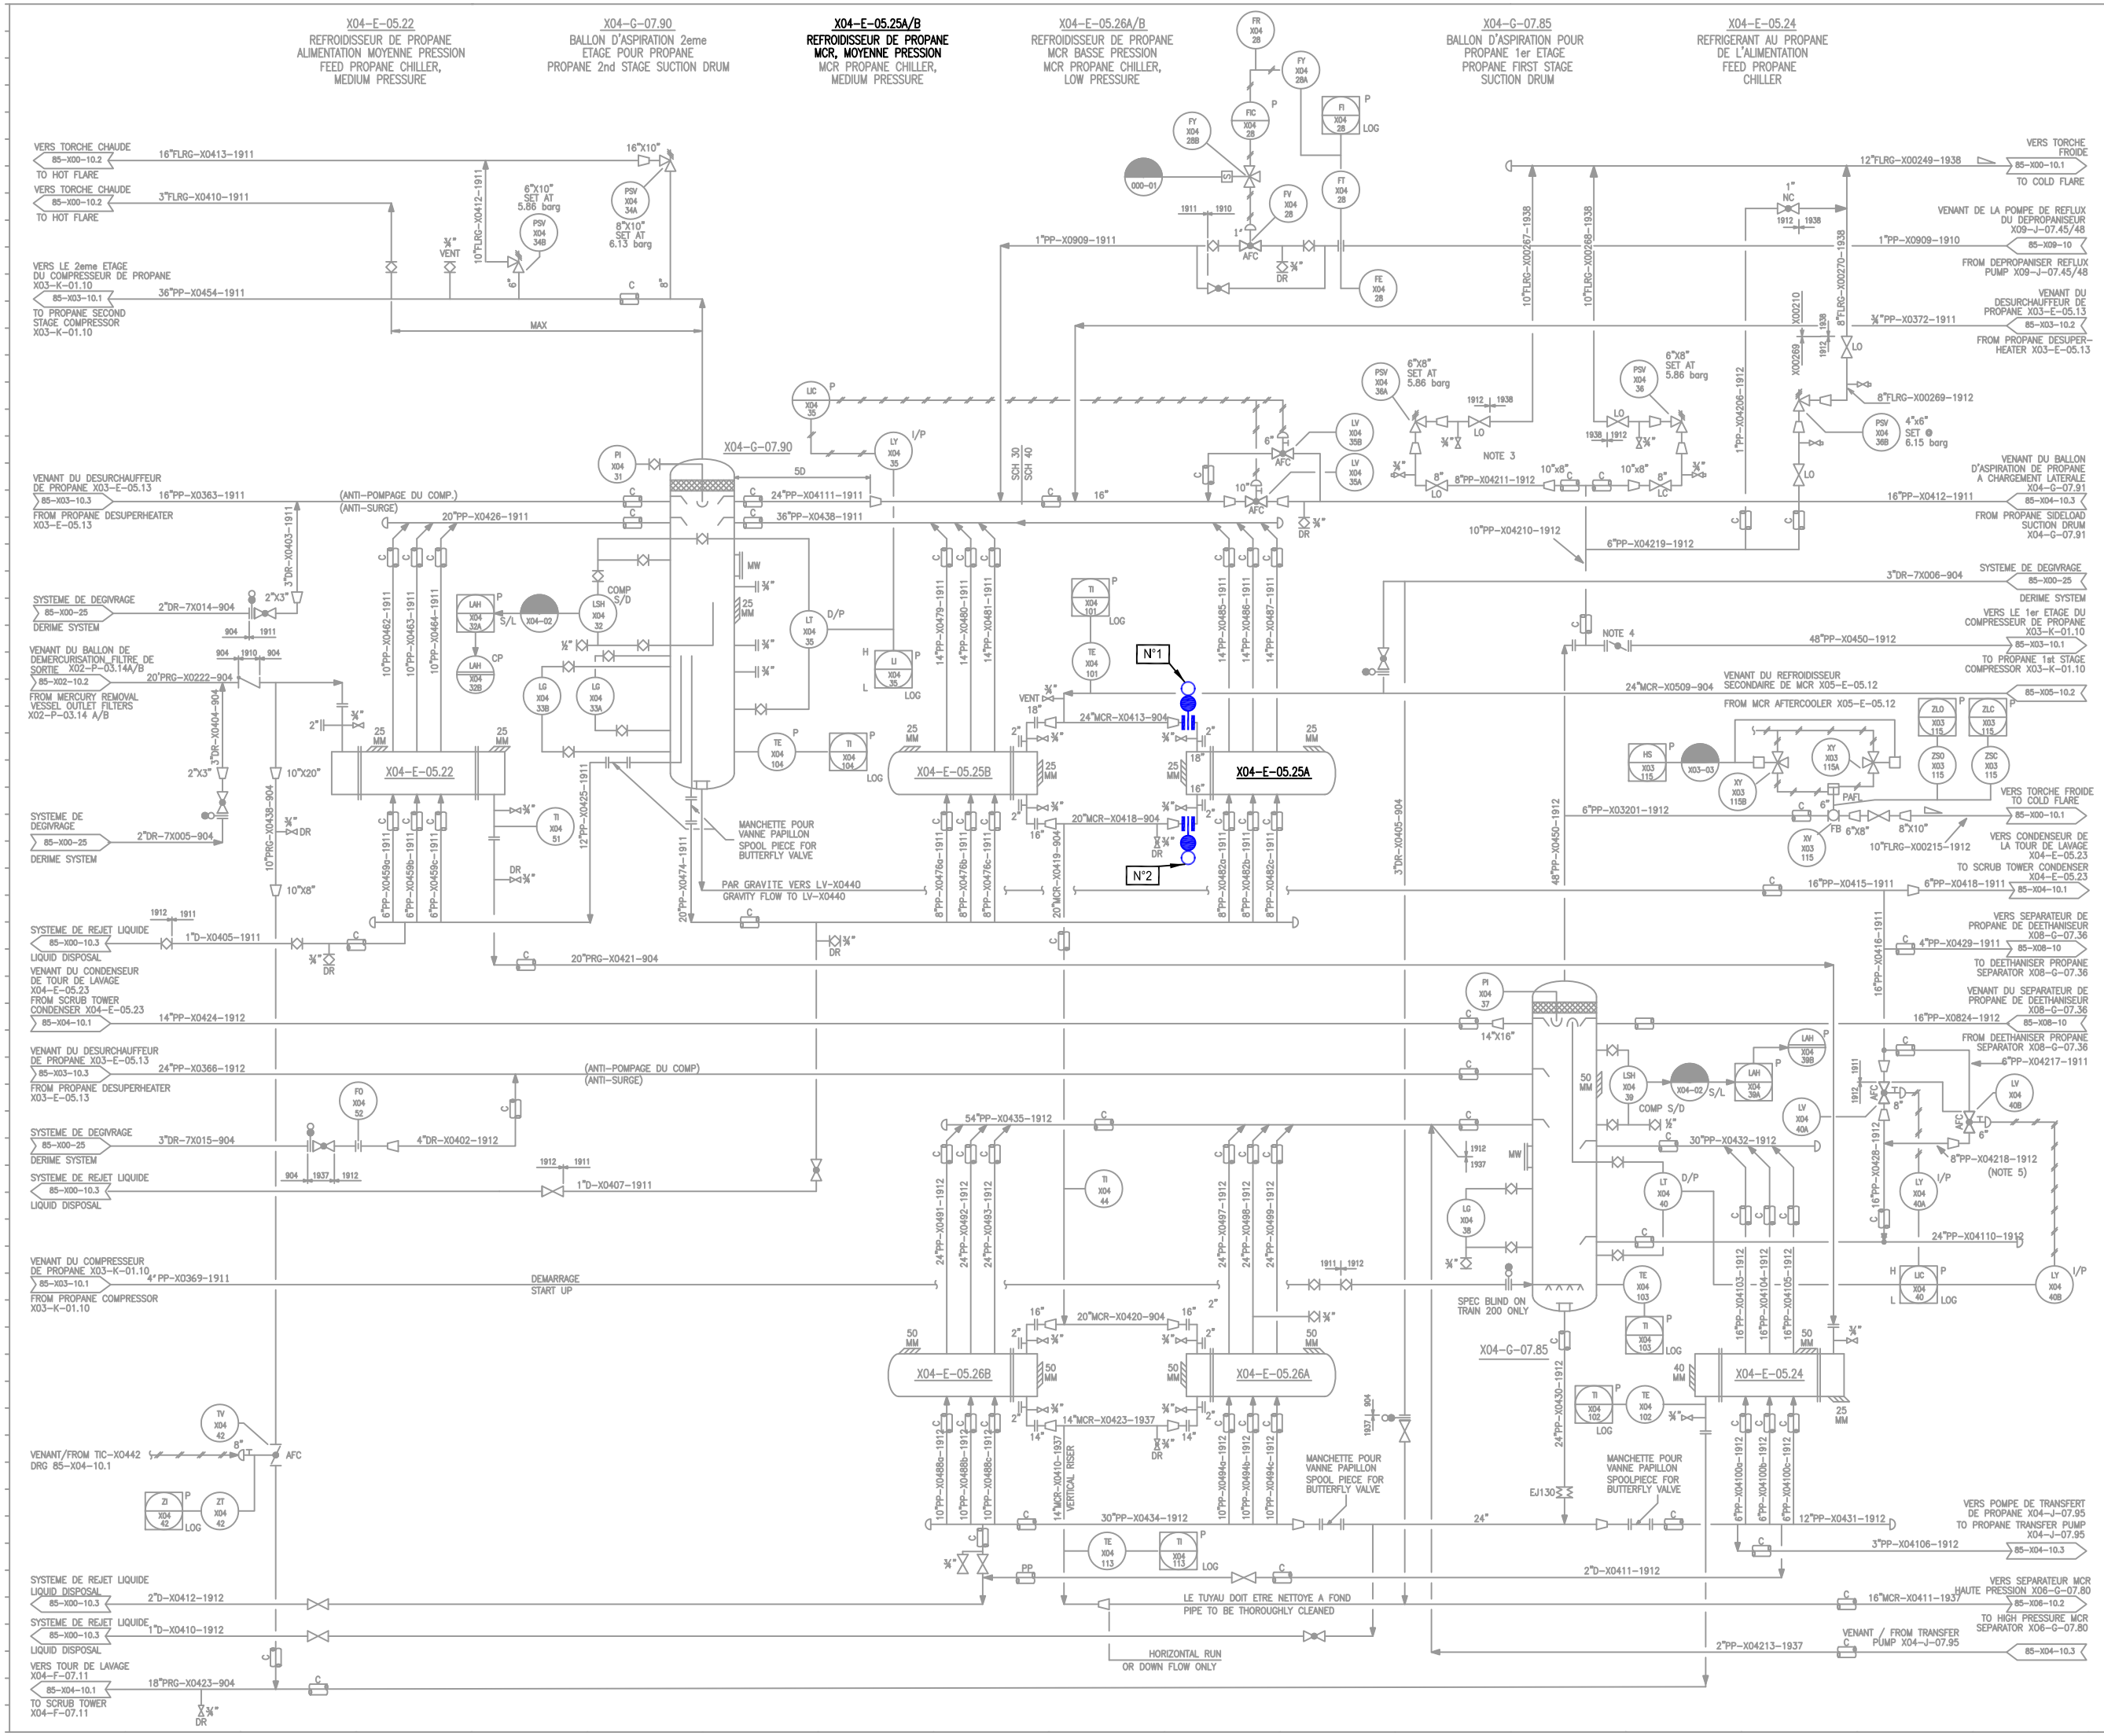

LISTE DES BRIDES D'ISOLEMENT

Brides N°	Localisation du plan de bride	N° de ligne	Spec.	Diam. de la bride	Observation
1	Entree MCR vers E-05.25A/B	24"MCR-X0413	904	18"	
2	Sortie MCR vers E-05.26A/B	20"MCR-X0418	904	16"	

PLAN DE REFERENCE

P&ID 85-X04-10.2

REV.	DATE	REVISION	BY	CHK	EPTG SUPV	DESIGN ENGR	PROJ ENGR	CLIENT
0	01-06-2006	EMIS POUR INSTALLATION	BB					

ECHELLE / SCALE: NONE | ETABLI / DRAWN: B.BOURA | VERIFIE / CHECKED:

S O N A T R A C H
ALGERIE

SONATRACH UNITE DE GNL
RENOVATION COMPLEXE GL1.Z
BETHIOUA, ALGERIE

SONATRACH LNG PLANT
GL1.Z RENOVATION
BETHIOUA, ALGERIA

PROCEDURE DE MISE SOUS JOINT PLEINS DE L'ECHANGEUR X04-E-05.25A

JOB N°	DRAWING N°	REV.
T-1087	DS X04-E-05.25A	0

PROCEDURE DE MISE SOUS JOINTS PLEINS DE L'ECHANGEUR (X04-E-05.25A) POUR TRAVAUX & INSPECTION

Bride N°	Localisation du plan de bride	N° de Ligne	Spécification des brides	Dimensions des brides	Observations	P&ID N°
1	Entrée MCR vers E-05.25A/B	24''MCR-X0413	904	18''		85-X04-10.2
2	Sortie MCR vers E-05.26A/B	20''MCR-X0418	904	16''		85-X04-10.2

	DATE	SIGNATURE
DEPARTEMENT TECHNIQUE	05/05/2014	
DEPARTEMENT PRODUCTION	12/05/14	