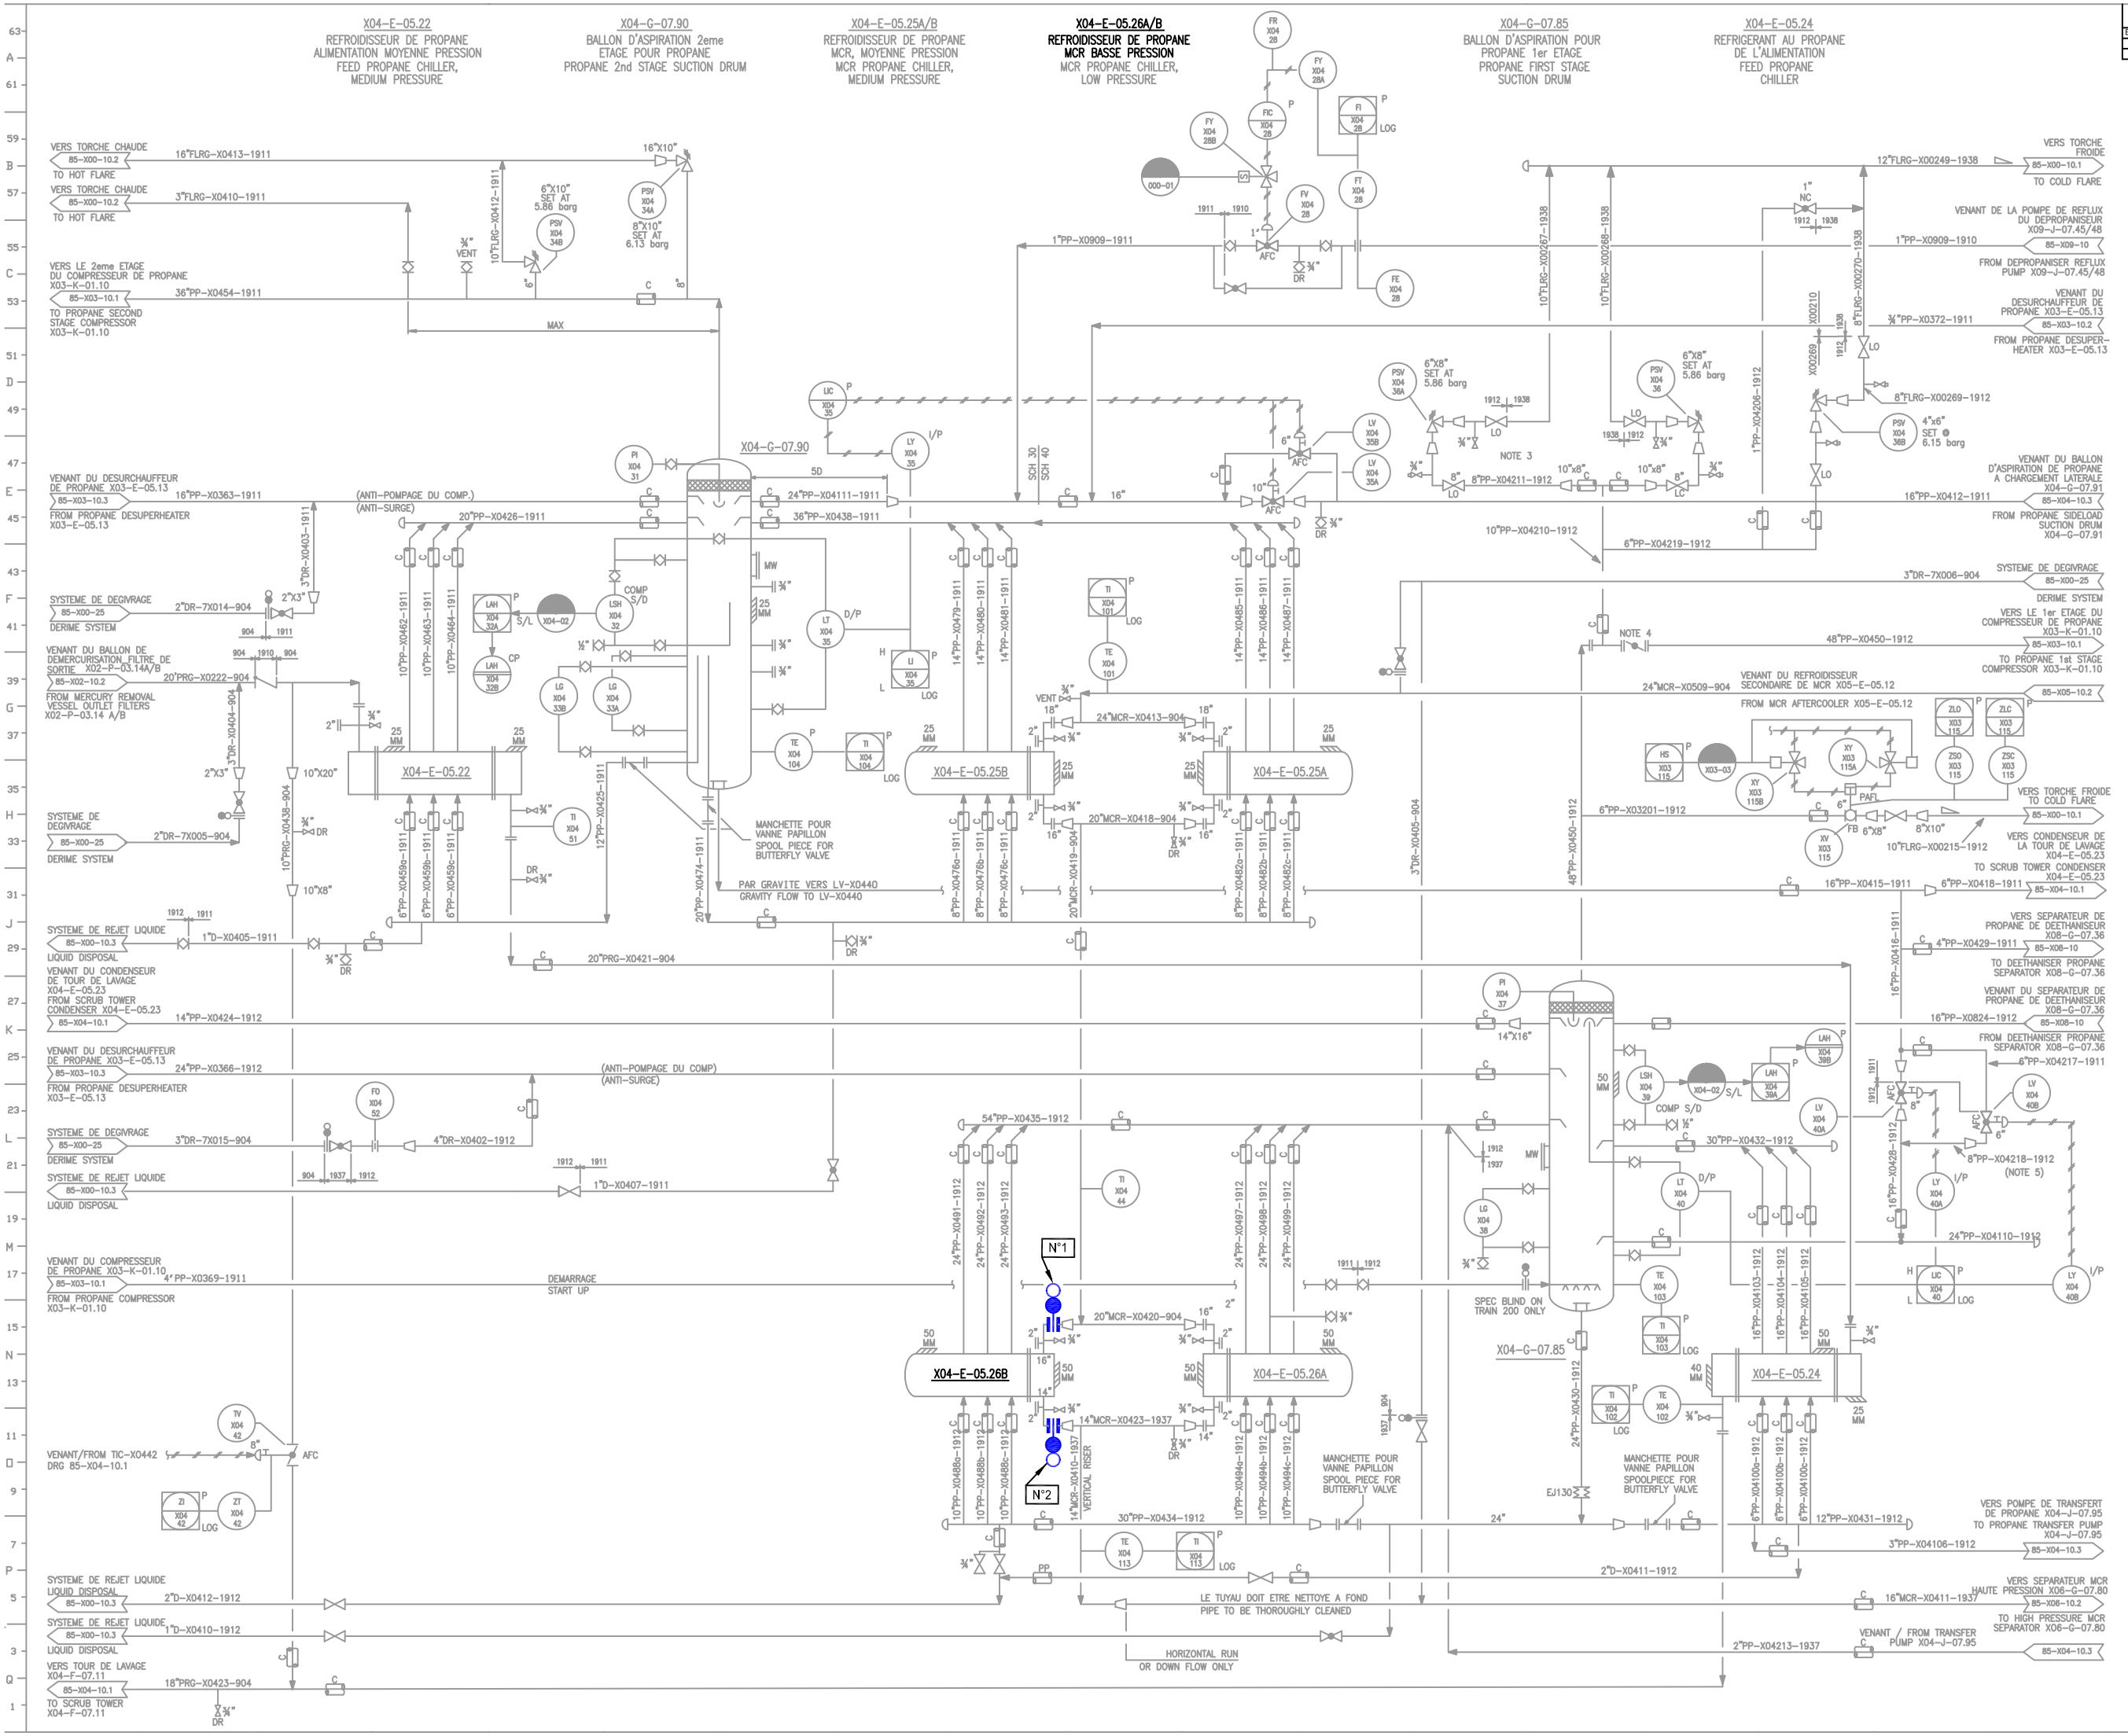


## LISTE DES BRIDES D'ISOLEMENT

| Brides N° | Localisation du plan de bride | N° de ligne | Spec. | Diam. de la bride | Observation |
|---|---|---|---|---|---|
| 1 | Entrée MCR vers E-05.26A/B | 20"MCR-X0420 | 904 | 16" | |
| 2 | Sortie MCR vers G-07.80 | 14"MCR-X0418 | 1937 | 14" | |

## PLAN DE REFERENCE

P&ID 85-X04-10.2

| REV. | DATE | REVISION | BY | CHK | OPTO SUPV | DESIGN MANAGER | PROJ. ENGR | CLIENT |
|---|---|---|---|---|---|---|---|---|
| 0 | 21-05-2002 | EMIS POUR INSTALLATION | BB | | | | | |

ECHELLE / SCALE: NONE — ETABLI / DRAWN: B.BOURA — VERIFIE / CHECKED:

**S O N A T R A C H**
ALGERIE

SONATRACH UNITE DE GNL — SONATRACH LNG PLANT
RENOVATION COMPLEXE GL1.Z — GL1.Z RENOVATION
BETHIOUA, ALGERIE — BETHIOUA, ALGERIA

**PROCEDURE DE MISE SOUS JOINT PLEINS DE L'ECHANGEUR XO4-E-05.26B**

| JOB N° | DRAWING N° | REV. |
|---|---|---|
| T-1087 | DS X04-E-05.26B | 0 |

# PROCEDURE DE MISE SOUS JOINTS PLEINS DE L'ECHANGEUR (X04-E-05.26B) POUR TRAVAUX & INSPECTION

| Bride N° | Localisation du plan de bride | N° de Ligne | Spécification des brides | Dimensions des brides | Observations | P&ID N° |
|---|---|---|---|---|---|---|
| 1 | Entrée MCR vers E-05.26A/B | 20''MCR-X0420 | 904 | 16'' | | 85-X04-10.2 |
| 2 | Sortie MCR vers G-07.80 | 14''MCR-X0423 | 1937 | 14'' | | 85-X04-10.2 |

| | DATE | SIGNATURE |
|---|---|---|
| DEPARTEMENT TECHNIQUE | 05/05/2014 | |
| DEPARTEMENT PRODUCTION | 12/05/14 | |