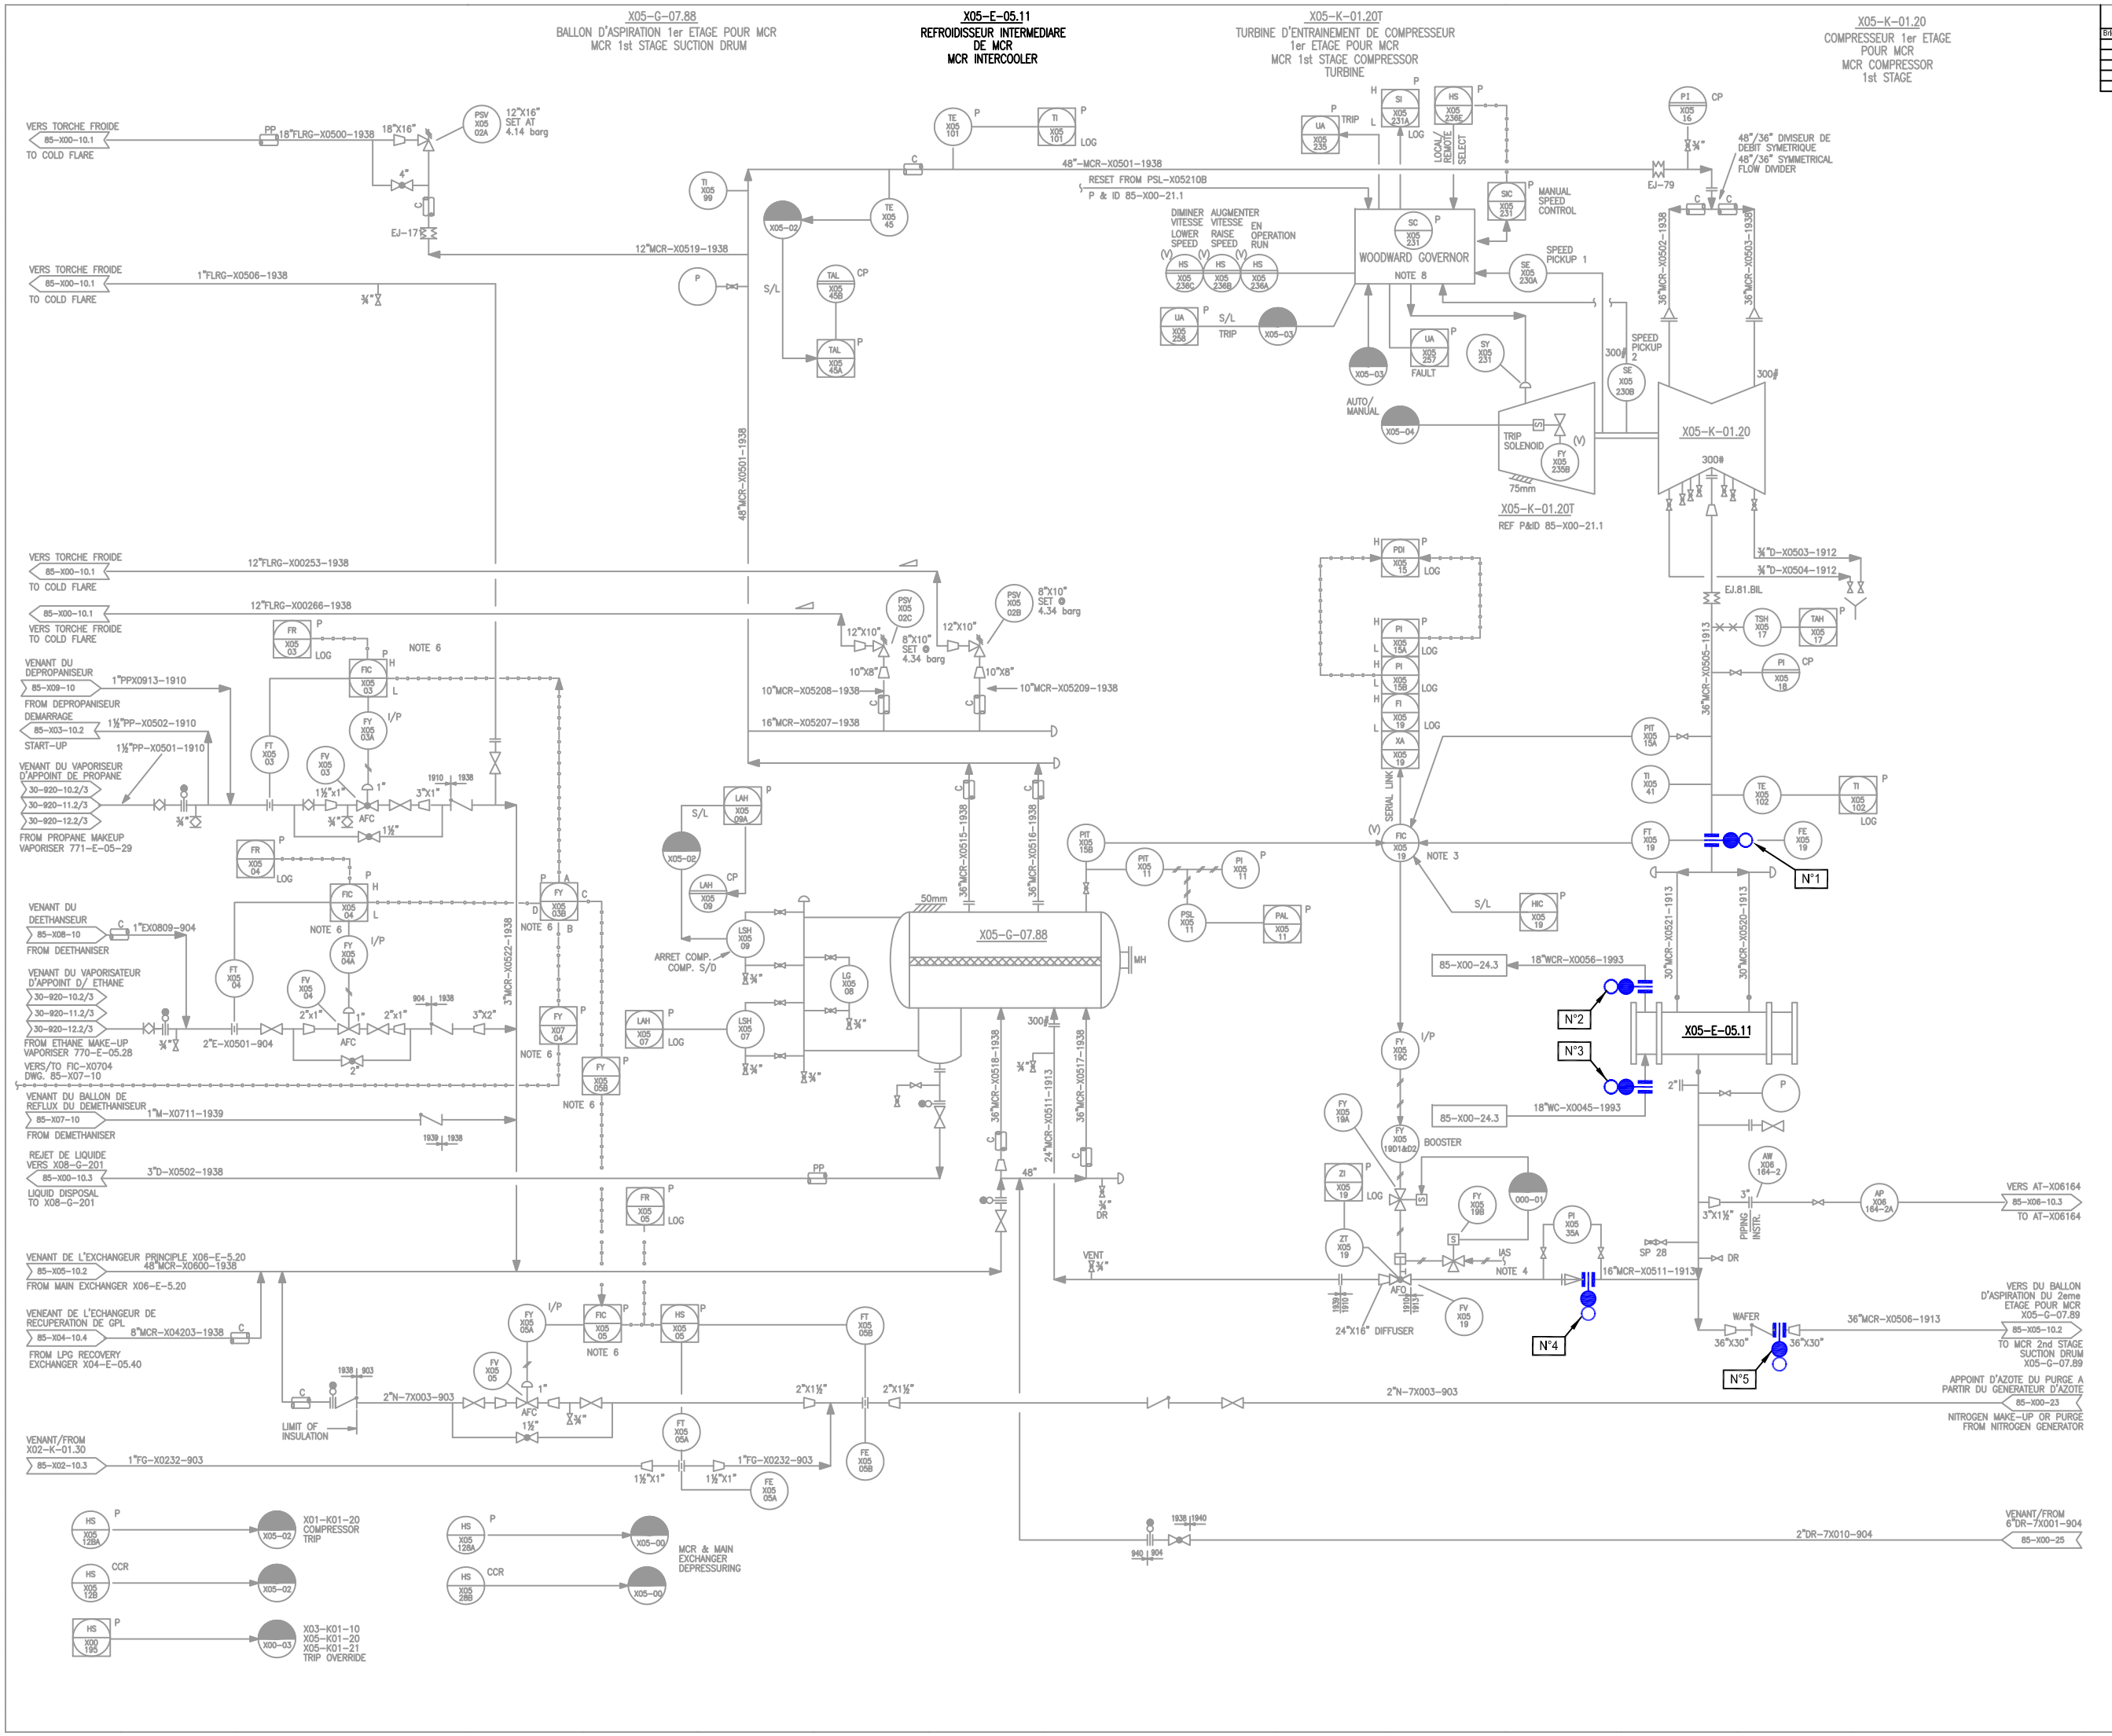

LISTE DES BRIDES D'ISOLEMENT

Brides N°	Localisation du plan de bride	N° de ligne	Spec.	Diam. de la bride	Observation
1	Entrée MCR vers E-05.11	36"MCR-X0505	1913	36"	
2	Sortie E.D.M.	18"WCR-X0056	1993	18"	
3	Entrée E.D.M. vers E-05.11	18"WC-X0045	1993	18"	
4	Sortie MCR vers G-07.88	16"MCR-X0511	1913	16"	
5	Sortie MCR vers G-07.89	36"MCR -X0506	1913	36"	

PLAN DE REFERENCE

P&ID 85-X05-10.1

REV.	DATE	REVISION	BY	CHK	OPTO SUPV	DES'N ENGEN	PROJ ENGEN	CLIENT
0	18-05-2005	EMS POUR INSTALLATION	BB					

ECHELLE / SCALE: NONE — ETABLI / DRAWN: B.BOURA — VERIFIE / CHECKED

S O N A T R A C H

ALGERIE

SONATRACH UNITE DE GNL
RENOVATION COMPLEXE GL1.Z
BETHIOUA, ALGERIE

SONATRACH LNG PLANT
GL1.Z RENOVATION
BETHIOUA, ALGERIA

PROCEDURE DE MISE SOUS JOINT PLEINS DE L'ECHANGEUR X05-E-05.11

JOB N°	DRAWING N°	REV.
T-1087	DS X05-E-05.11	0

PROCEDURE DE MISE SOUS JOINTS PLEINS DE L'ECHANGEUR (X05-E-05.11) POUR TRAVAUX & INSPECTION

Bride N°	Localisation du plan de bride	N° de Ligne	Spécification des brides	Dimensions des brides	Observations	P&ID N°
1	Entrée MCR vers E-05.11	36'' MCR-X0505	1913	36''		85-X05-10.1
2	Sortie E.D.M.	18''WCR-X0056	1993	18''		85-X05-10.1
3	Entrée E.D.M. vers E-05.11	18''WC-X0045	1993	18''		85-X05-10.1
4	Sortie MCR vers G-07.88	16''MCR-X0511	1913	16''		85-X05-10.1
5	Sortie MCR vers G-07.89	36''MCR-X0506	1913	30''		85-X05-10.1

	DATE	SIGNATURE
DEPARTEMENT TECHNIQUE	11/05/2014	
DEPARTEMENT PRODUCTION	11/05/14	