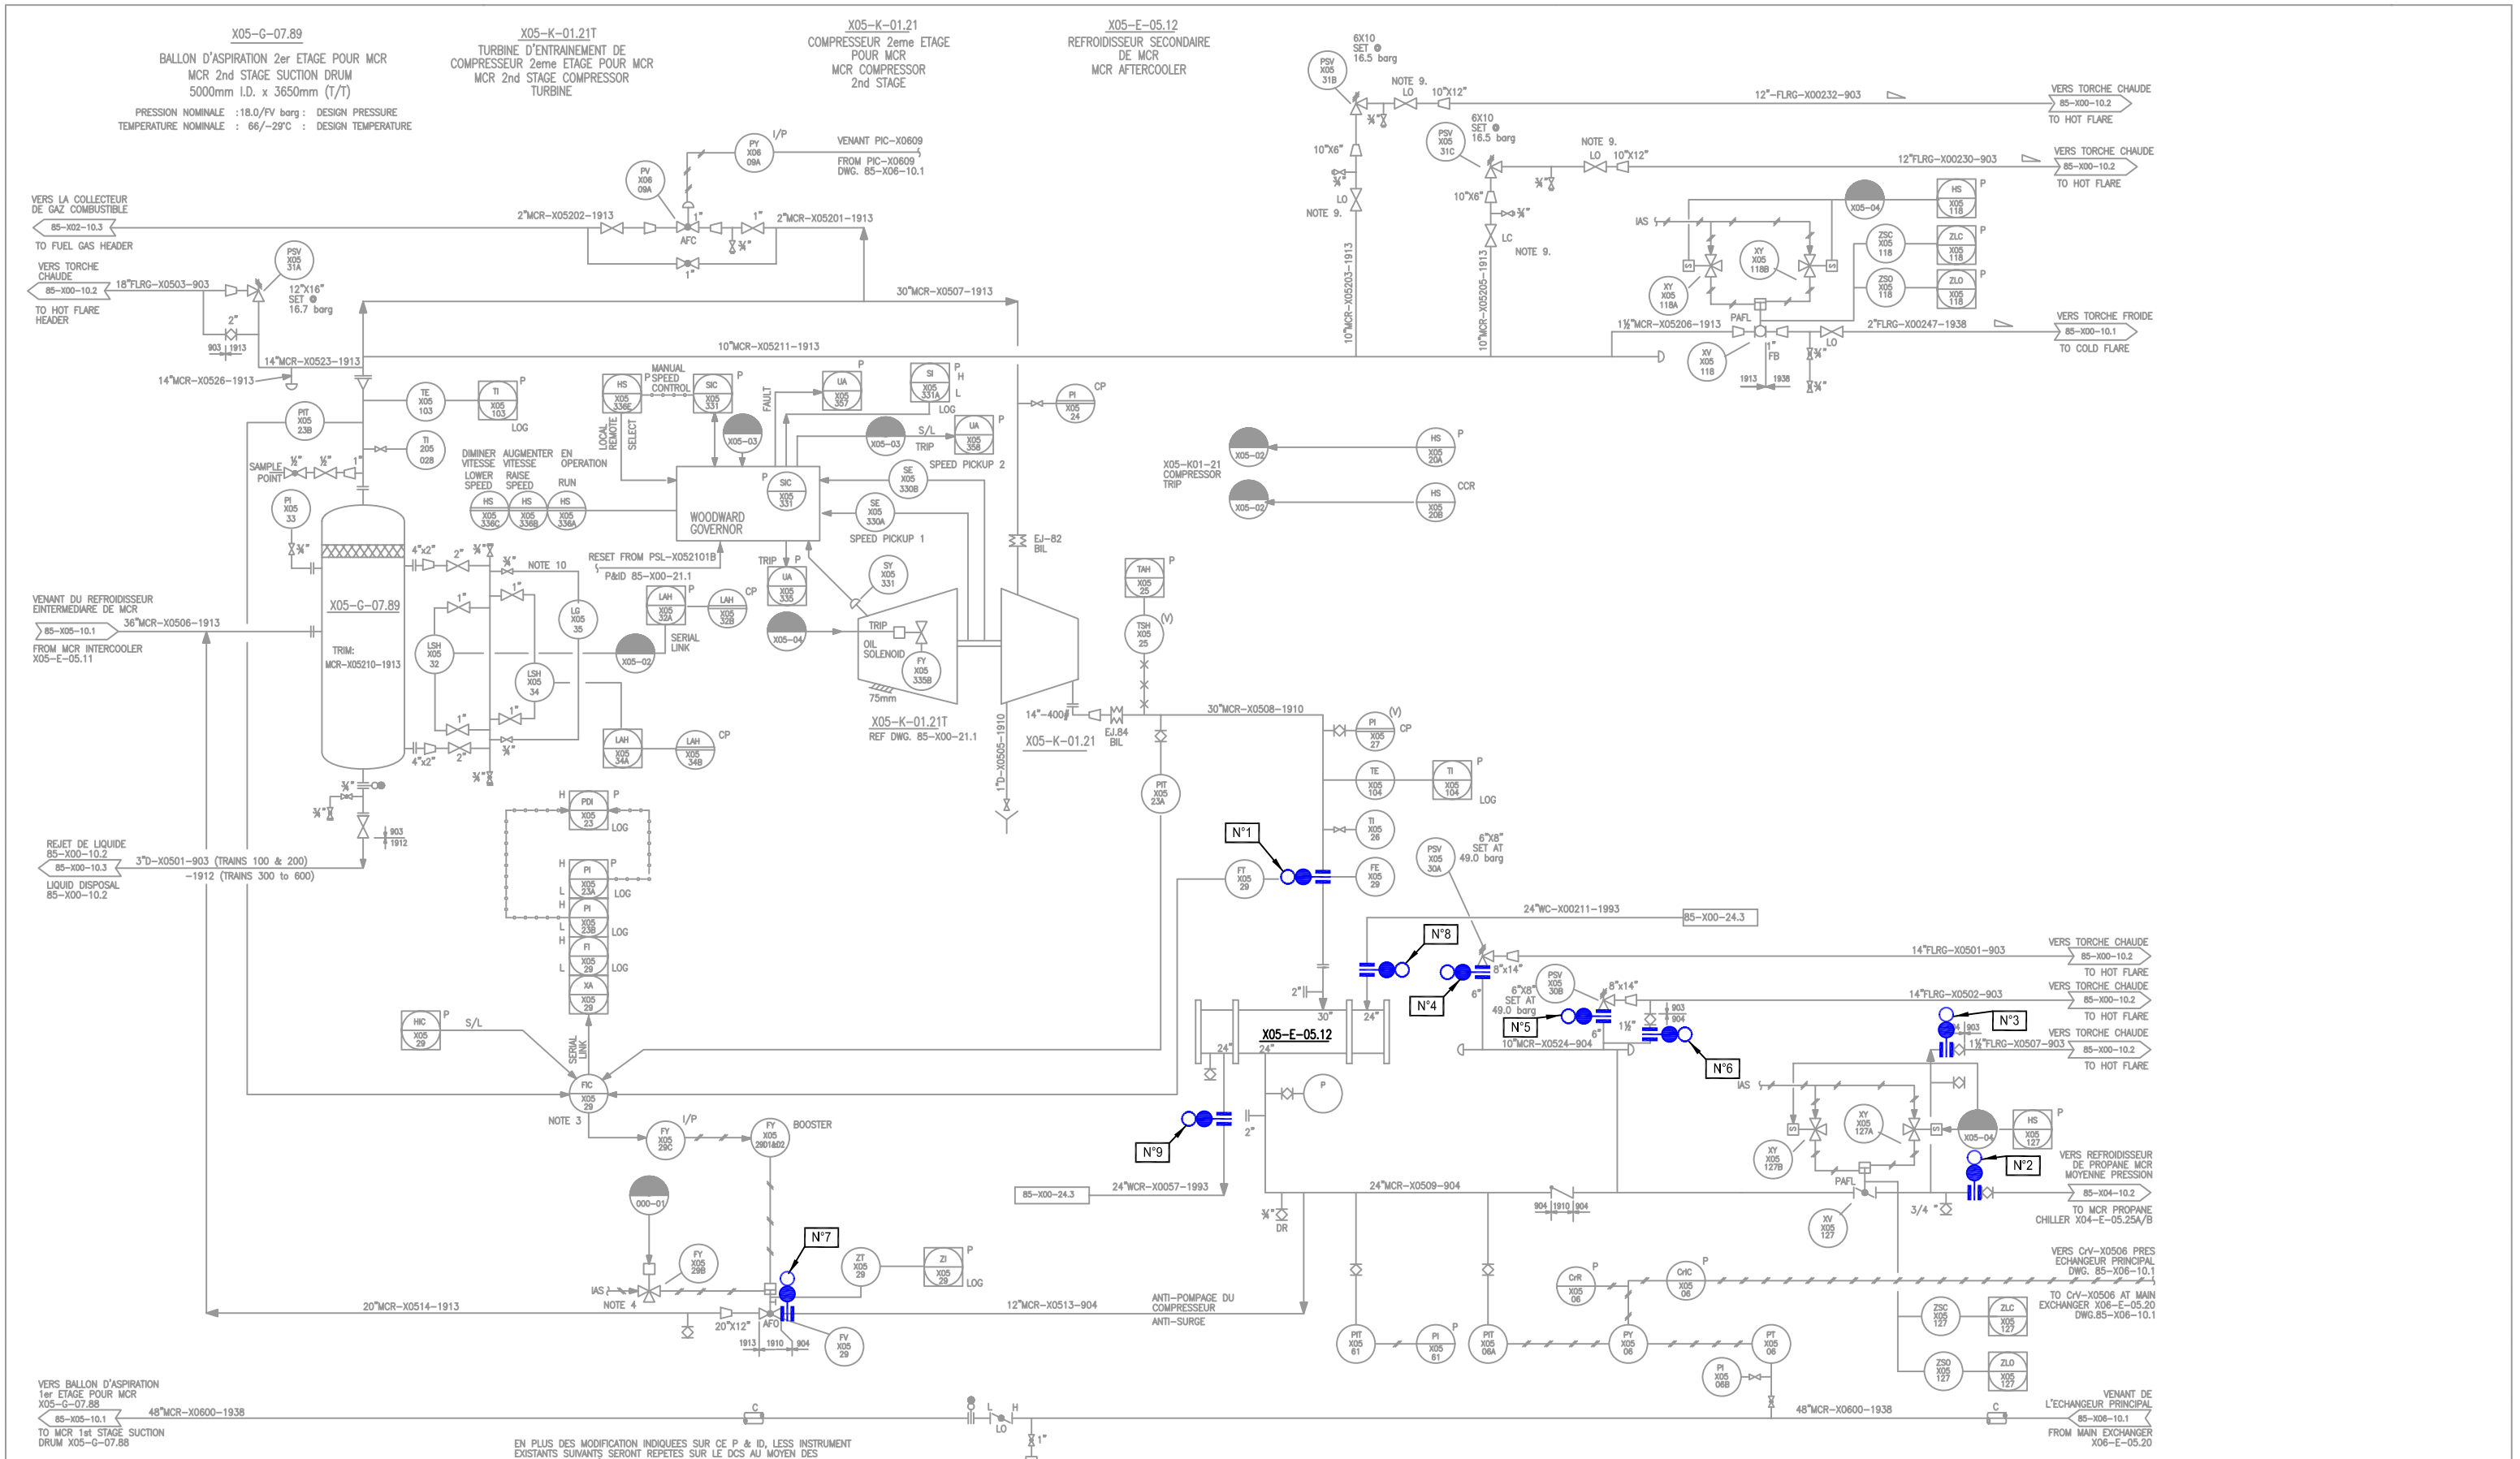

EN PLUS DES MODIFICATION INDIQUEES SUR CE P & ID, LESS INSTRUMENT EXISTANTS SUIVANTS SERONT REPETES SUR LE DCS AU MOYEN DES RACCORDEMENTS D'INSTRUMENTS DETAILES CI-DESSOUS:-

(SUITE SUR P&ID 85-X05-10.1)

IN ADDITION TO THE INSTRUMENTATION CHANGES SHOWN IN THE BODY OF THIS P & ID, THE FOLLOWING EXISTING INSTRUMENTS WILL BE REPEATED ON THE DCS BY WAY OF THE INSTRUMENT TIE-INS DETAILED BELOW:-

(CONTINUED ON P&ID 85-X05-10.1)

	NUMERO DE SONDE	NOUVEAU PROXIMETRE	NOUVEL INDICATEUR	NUMERO DE DCS	ALARME PANNEAU LOCAL	NUMERO DE DCS	DETAIL	NUMERO DE DESIGN
	PROBES TAG No.	NEW PROXIMETER TAG No. A	NEW INDICATOR TAG No. B	DCS TAG No. C	LOCAL PANEL ALARM TAG No. D	DCS TAG NO. E	DETAIL	DRG. No. (PACKAGED)
	COMPRESSEUR 1ER ETAGE POUR MCR/MCR COMPRESSOR 1ST STAGE X05-K-01.20							
SONDES EXISTANTES EXISTING PROBES	XE-X1321X XE-X1321Y XE-X1322X XE-X1322Y ZE-X1323	XT-X1321X XT-X1321Y XT-X1322X XT-X1322Y ZT-X1323	XI-X1321X XI-X1321Y XI-X1322X XI-X1322Y ZI-X1323	XI-X1321XA XI-X1321YA XI-X1322XA XI-X1322YA ZI-X1323A ZI-X1334A XAH-X1321X XAH-X1321Y XAH-X1322X XAH-X1322Y ZAH-X1323A ZAH-X1334 ZA-X1323 ZAH-X1323	– – – –

PROCEDURE DE MISE SOUS JOINTS PLEINS DE L'ECHANGEUR (X05-E-05.12) POUR TRAVAUX & INSPECTION

Bride N°	Localisation du plan de bride	N° de Ligne	Spécification des brides	Dimensions des brides	Observations	P&ID N°
1	Entrée MCR vers E-05.12 au niveau du FT-529	30''MCR-X0508	1910	30''		85-X05-10.2
2	Sortie MCR vers E-05.25A/B Aval XV-127	24''MCR-X0509	904	24''		85-X05-10.
3	Ligne aval XV-127 vers torche	1 ½'' FLRG-X0507	903	1 ½"		85-X05-10.2
4	Ligne PSV X0530A	6" MCR-X0524	904	6"		85-X05-10.2
5	Ligne PSV X0530B	6'' MCR-X0524	904	6"		85-X05-10.2
6	Ligne de by-pass PSV X0530B	1 ½"	904	1 ½"		85-X05-10.2
7	Ligne anti pompage Amont FV-X0529	12" MCR-X0513	904	12"		85-X05-10.2
8	Entrée E.D.M.	24''WC-X00211	1993	24''		85-X05-10.2
9	Sortie E.D.M.	24''WCR-X0057	1993	24''		85-X05-10.2

	DATE	SIGNATURE
DEPARTEMENT TECHNIQUE	13/05/2014	
DEPARTEMENT PRODUCTION	15.05.14	