LISTE DES BRIDES D'ISOLEMENT

Brides N°	Localisation du plan de bride	N° de ligne	Spec.	Observation
1	Tête G-07.89	30"MCR-X0507	1913	Brider au niveau de la tubulure du ballon
2	Drain fond G-07.89	3"D-X0501	903/1912	Brider au niveau de la tubulure du ballon
3	Alimentation G-07.89	36"MCR-X0506	1913	Brider au niveau de la tubulure du ballon

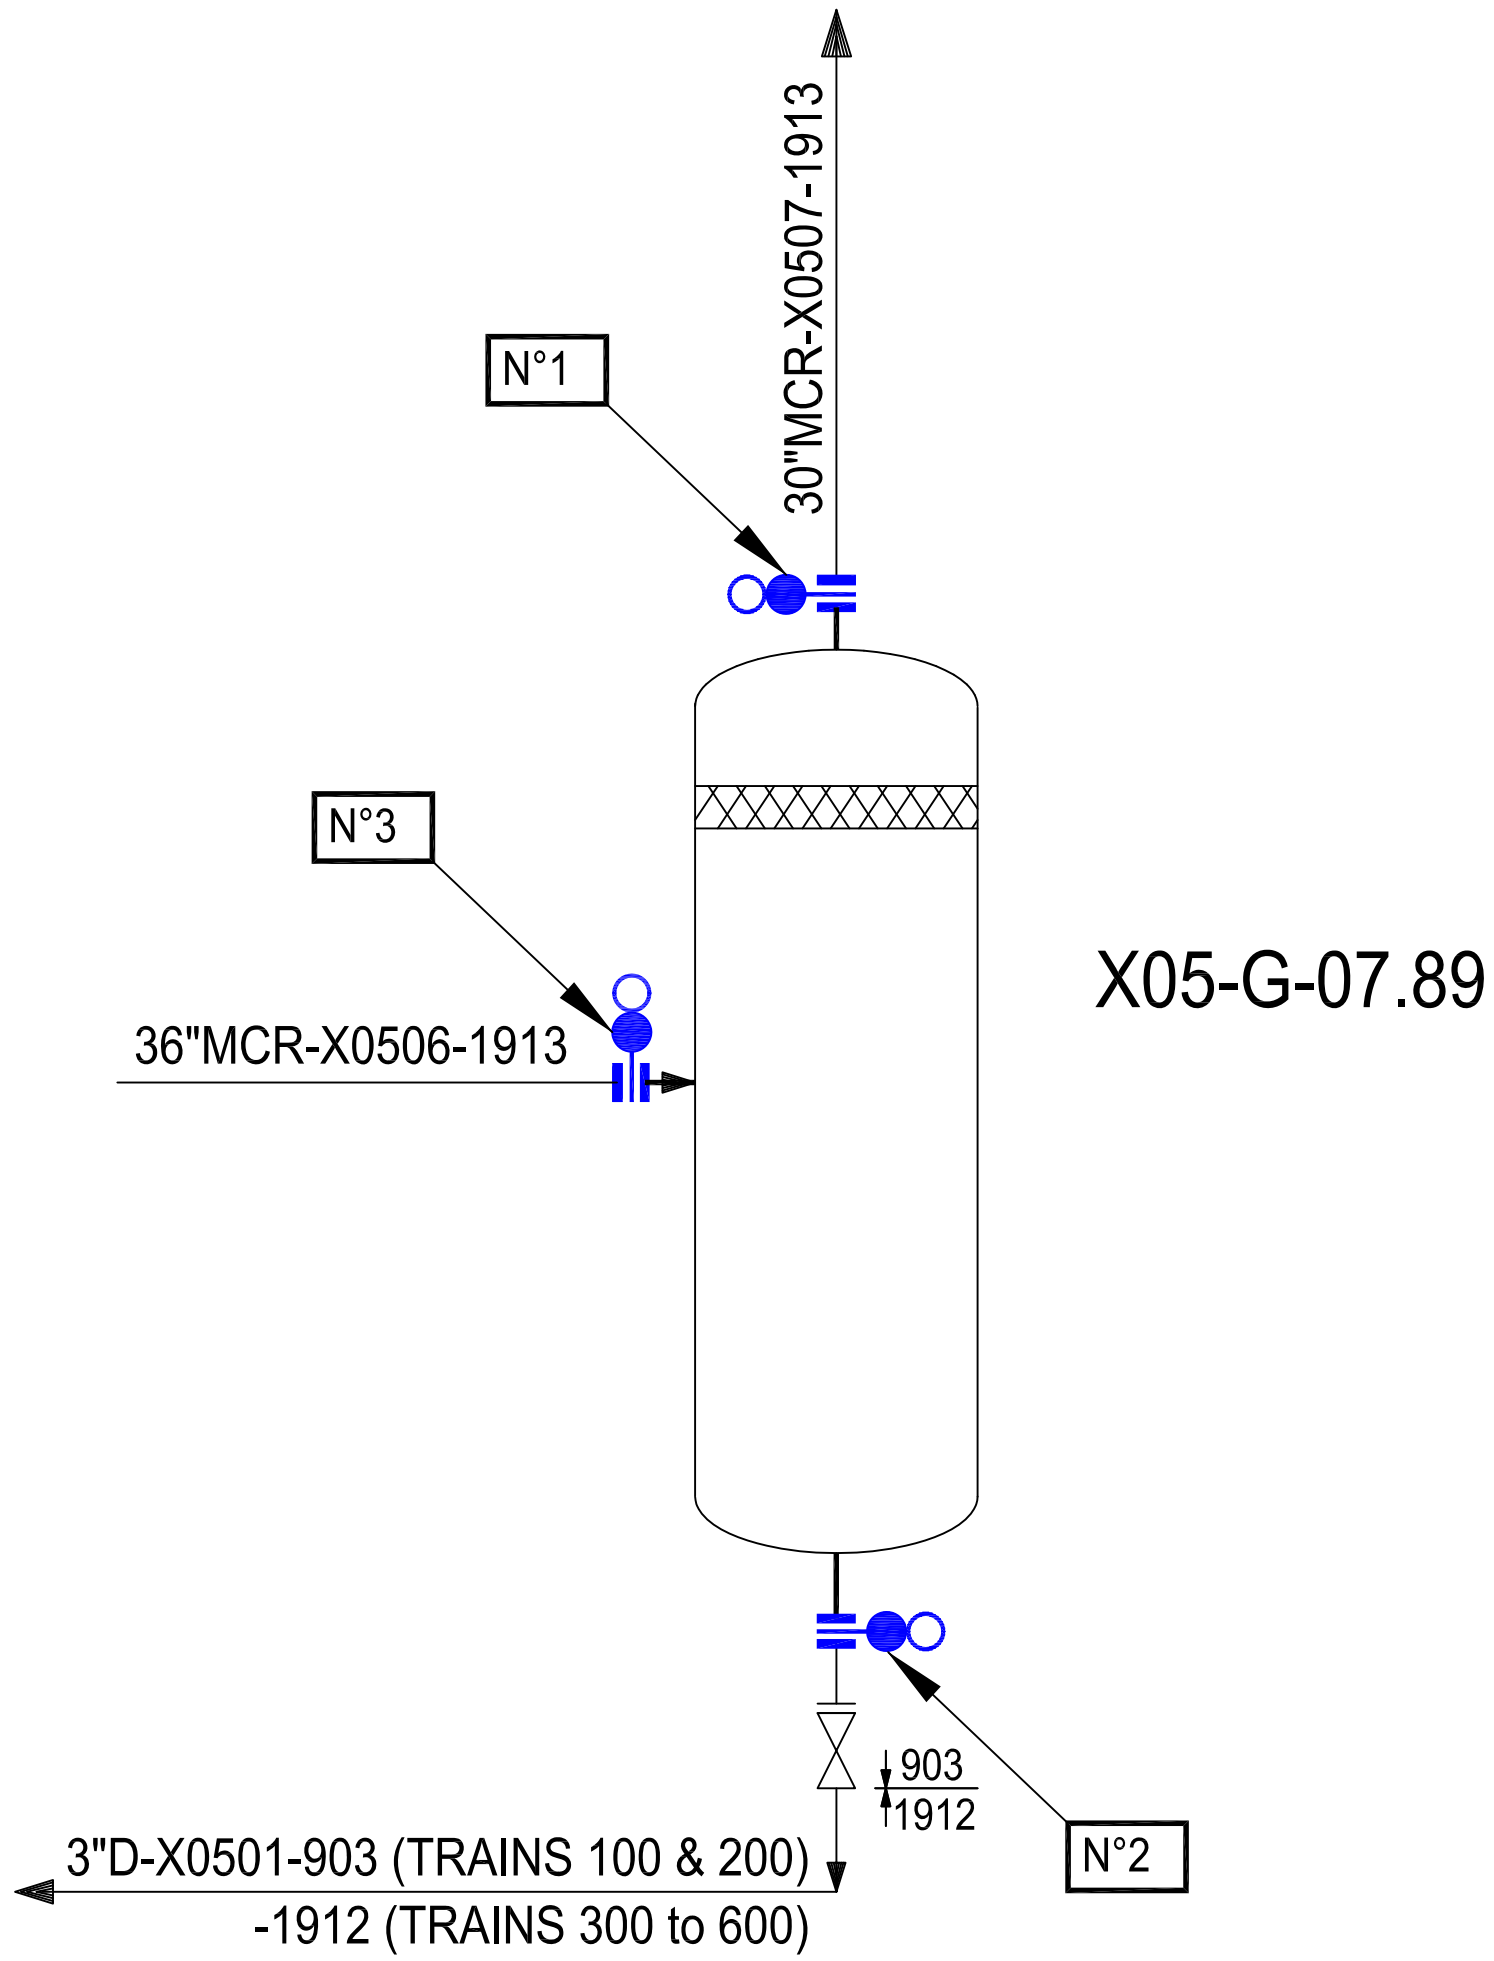

PLAN DE REFERENCE

P&ID 85-X05-10.2

REV.	DATE	REVISION	BY	CH'K	DFTG SUPV	DES'N ENG'R	PROJ ENG'R	CLIENT
0	23-06 2004	EMIS POUR INSTALLATION	BB					

ECHELLE / SCALE: NONE — ETABLI / DRAWN: B.BOURA — VERIFIE / CHECKED:

S O N A T R A C H

ALGERIE

SONATRACH UNITE DE GNL
RENOVATION COMPLEXE GL1.Z
BETHIOUA, ALGERIE

SONATRACH LNG PLANT
GL1.Z RENOVATION
BETHIOUA, ALGERIA

ISOLEMENT PAR SPECTACLE BLIND POUR PENETRATION DU X05-G-07.89

JOB N°	DRAWING N°	REV.
T-1087	X05-G-07.89	0

PROCEDURE DE MISE SOUS JOINTS PLEINS DU BALLON X05-G-07.89 POUR TRAVAUX & INSPECTION

Bride N°	Localisation de Plan de Bride	N° de Ligne	Spécification des brides	Dimensions des brides	Observations	P&ID N°
1	Tête G-789	30"MCR-X0507	1913	30"		85-X05-10.2
2	Drain fond G-789	3"D-X0501	1912	3"	Spec 903 : 100 & 200 Spec 1912 : 300 to 600	85-X05-10.2
3	Alimentation G-789	36"MCR-X0506	1913	36"		85-X05-10.2

	DATE	SIGNATURE
DEPARTEMENT TECHNIQUE	11/05/2014	
DEPARTEMENT PRODUCTION	11/05/14	